




MOVING HOUSE

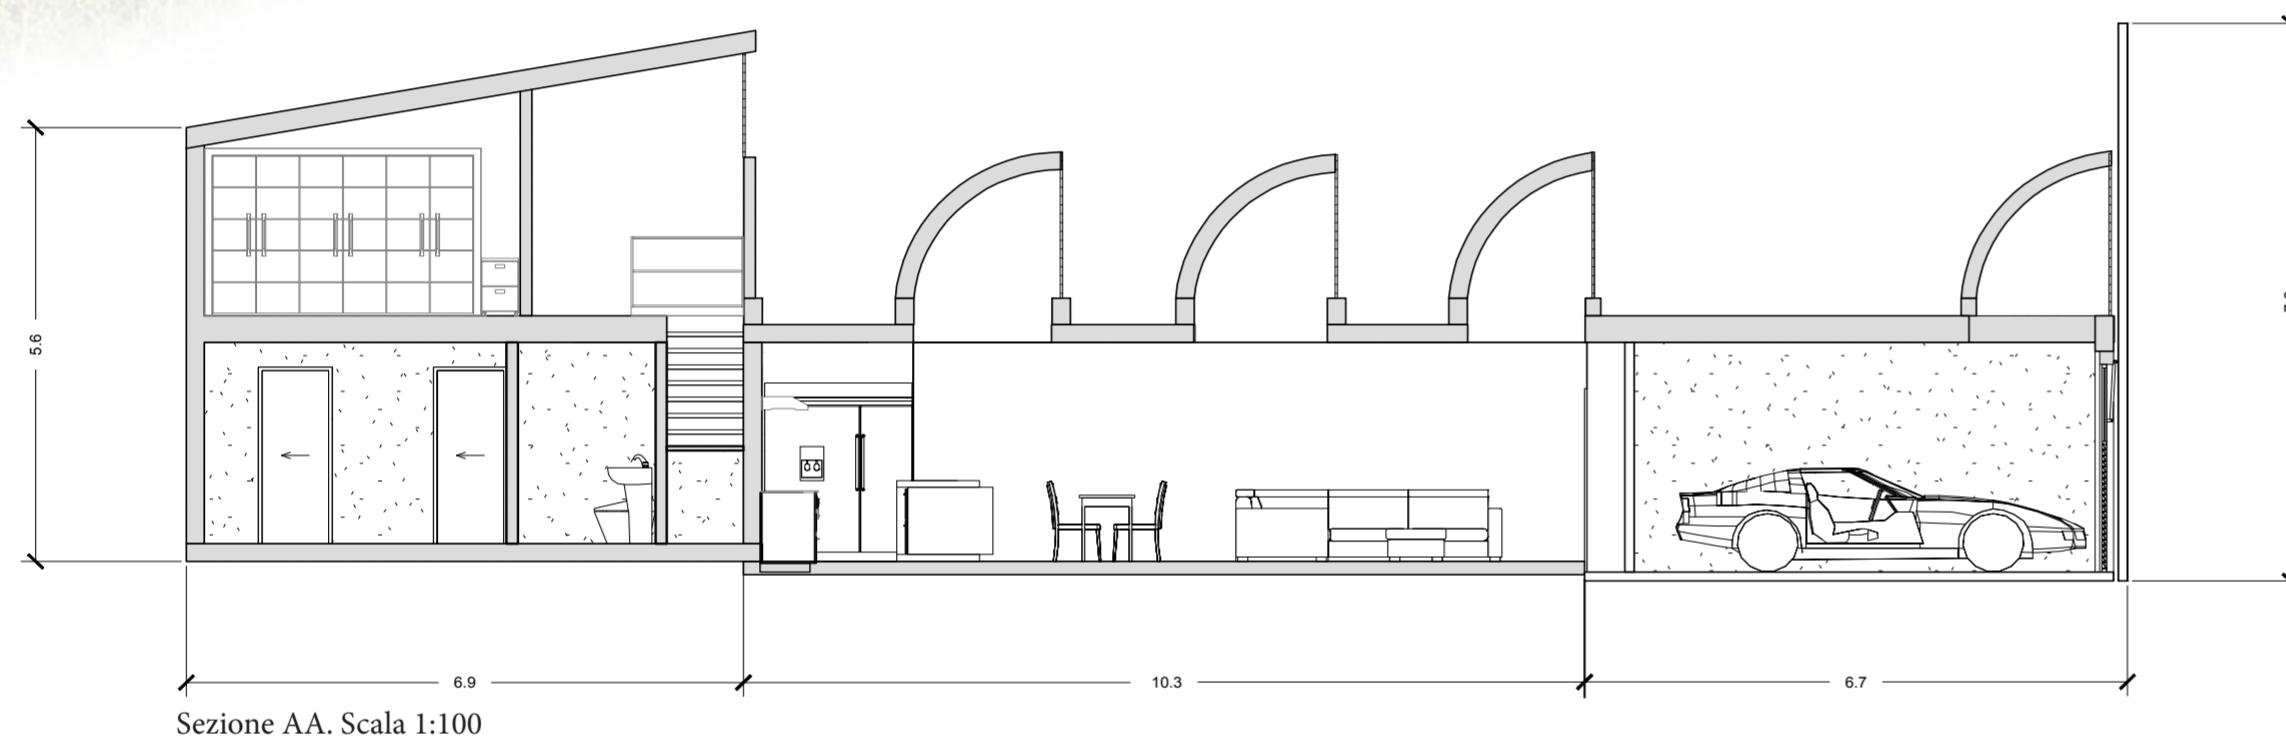


Sezione AA. Scala 1:100

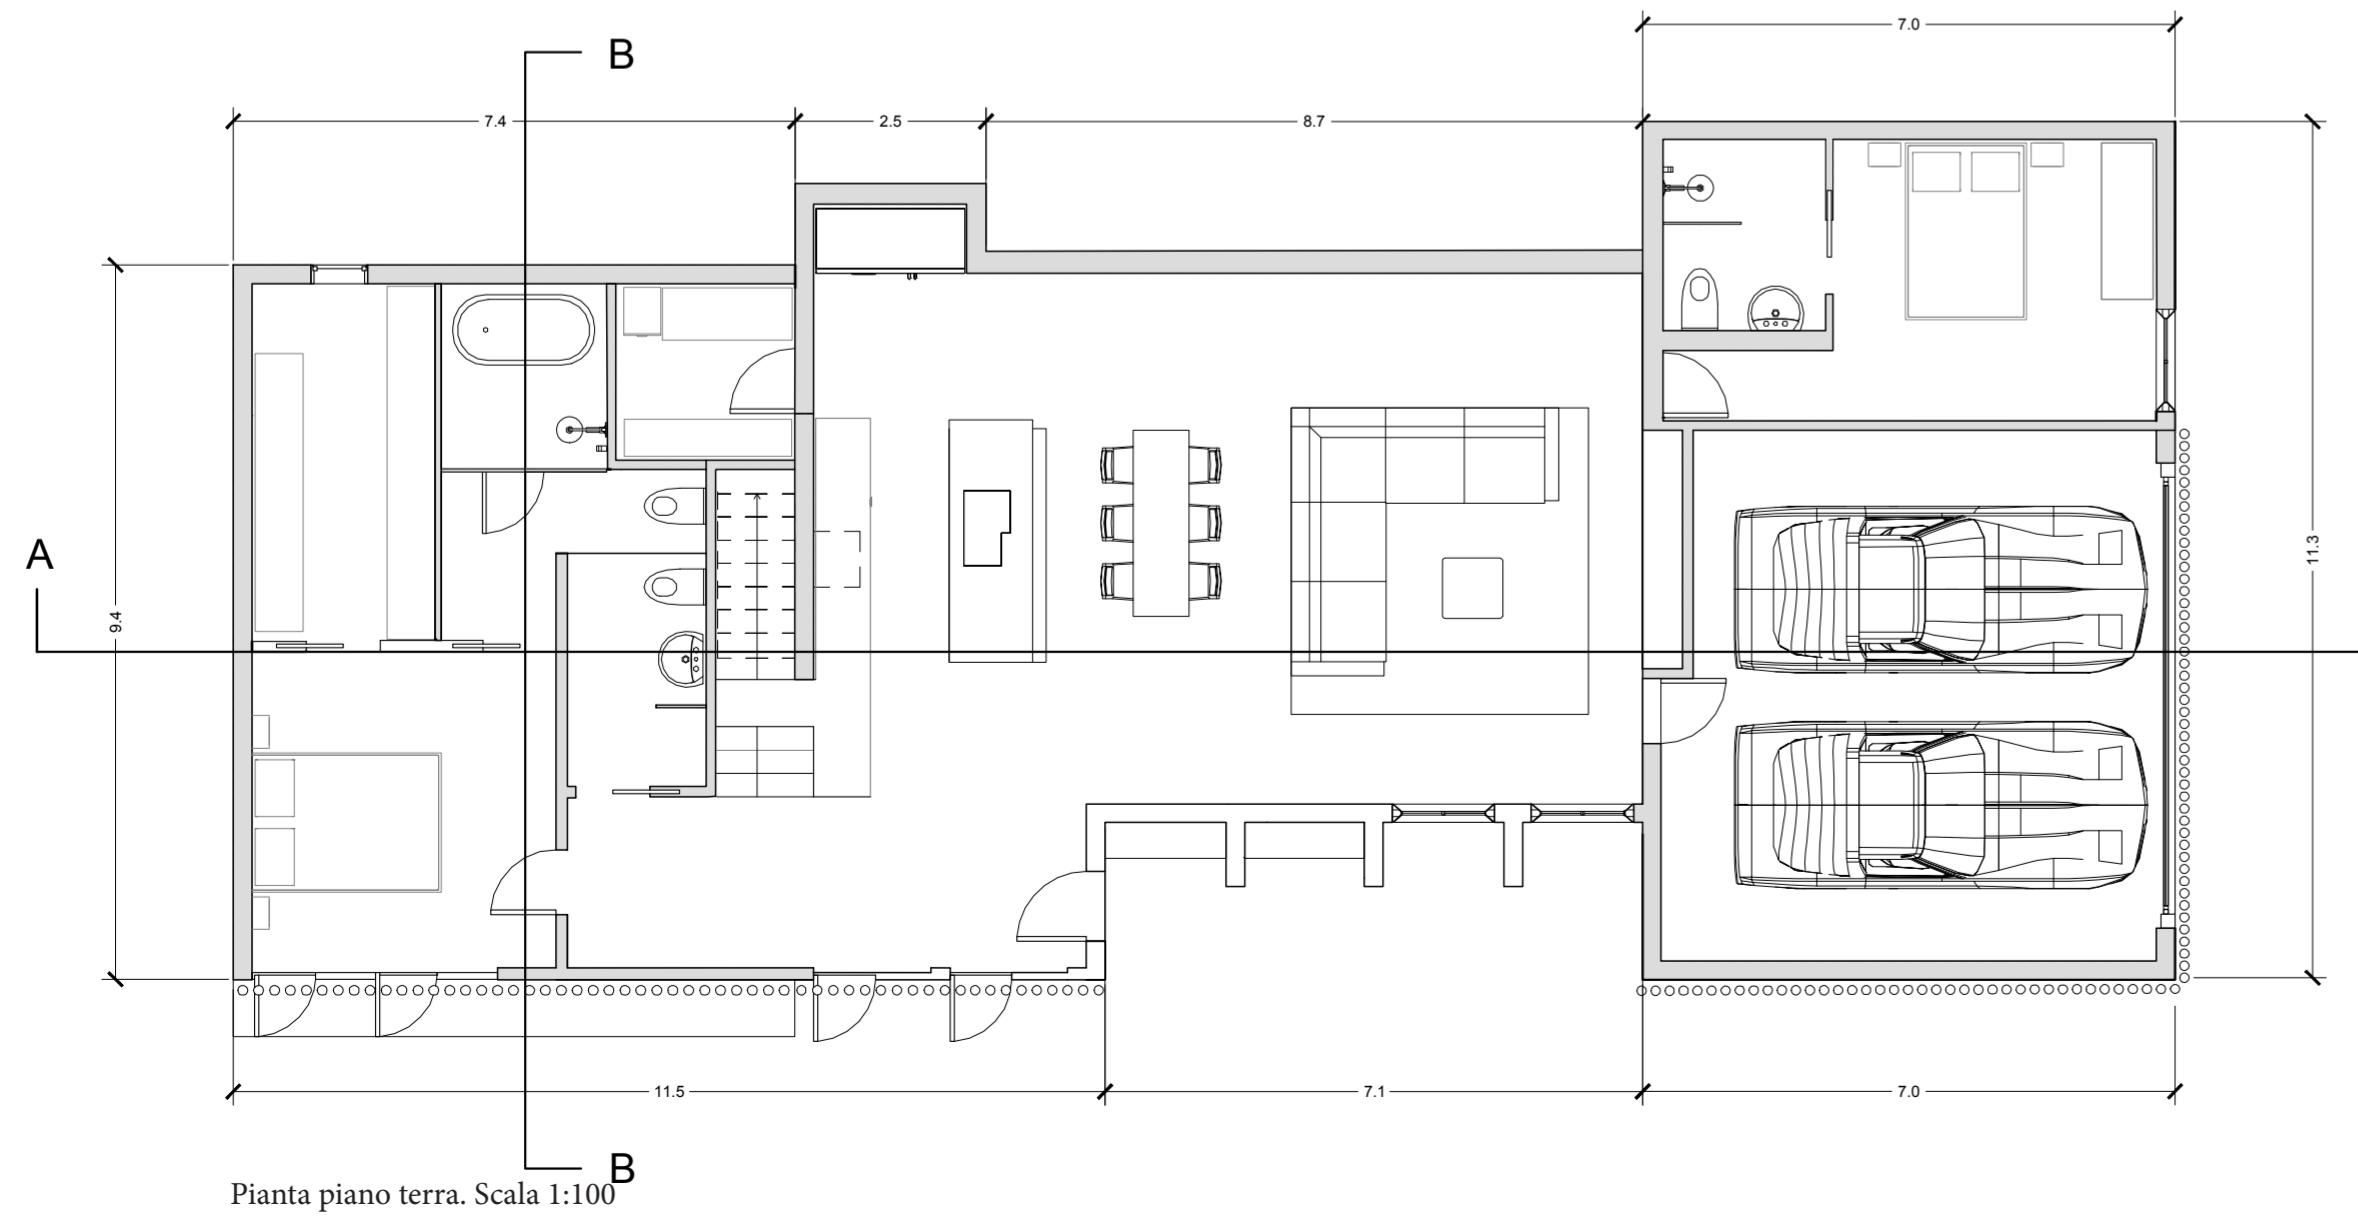


Pianta piano terra. Scala 1:100

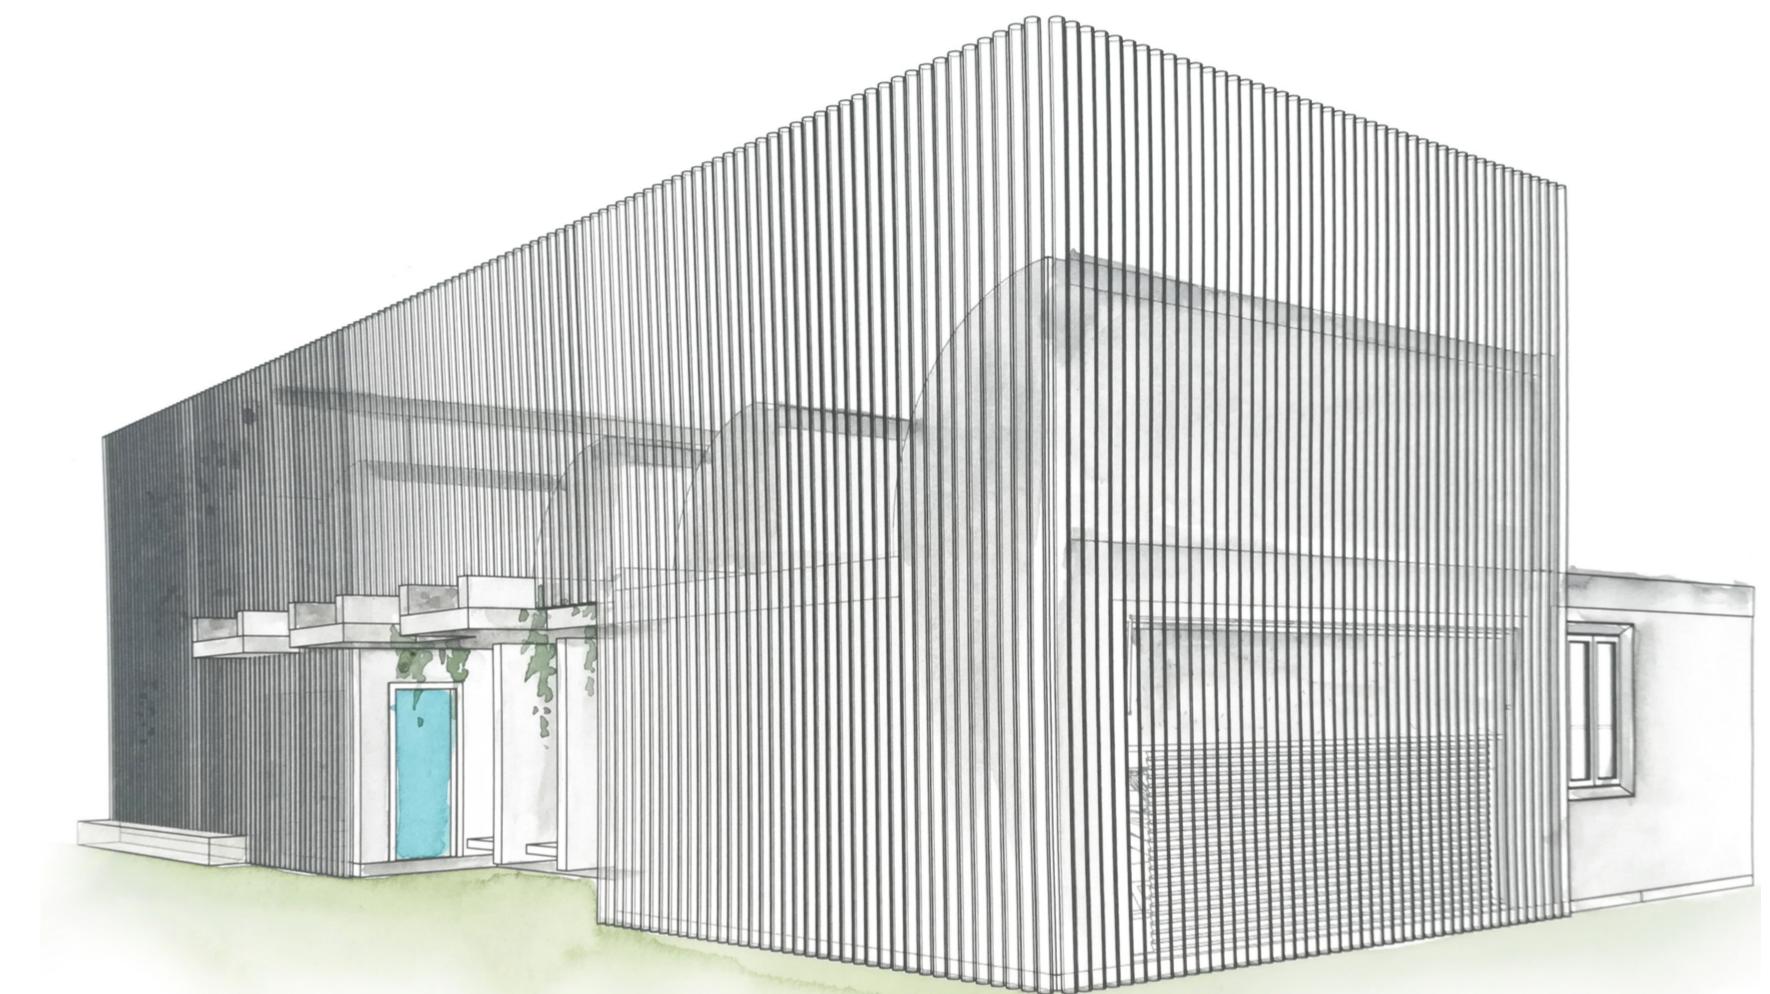


The Moving House è una residenza situata in Kew, Victoria, Australia. Il progetto è stato curato dal gruppo di architetti EAT nel 2016. È caratterizzato da linee pulite, ripetitive. Tutta la struttura è costituita da cemento armato lasciato a vista, che conferisce all'intero edificio un aspetto crudo e profondamente essenziale. L'elemento maggiormente caratterizzante dell'architettura è sicuramente lo schermo generato da numerosi pilastri in alluminio che accostati l'uno all'altro, coprono e al tempo stesso lasciano trasparire la singolare forma della struttura. I tetti in particolare sono costituiti da volte in cemento armato che fungono da lucernai e donano immensa luminosità e senso di apertura alla zona living. Gli interni rispecchiano la filosofia alla base del progetto: rigore e pulizia. Forte attenzione viene dedicata alla scelta degli elementi d'arredo, i quali devono spiccare e al tempo stesso mantenersi in continuità con le pavimentazioni lasciate grezze. L'aspetto complessivo è di armonia e coesione, semplicità e praticità. Massima pulizia di scelta e di linea, in forte dialogo con la natura.

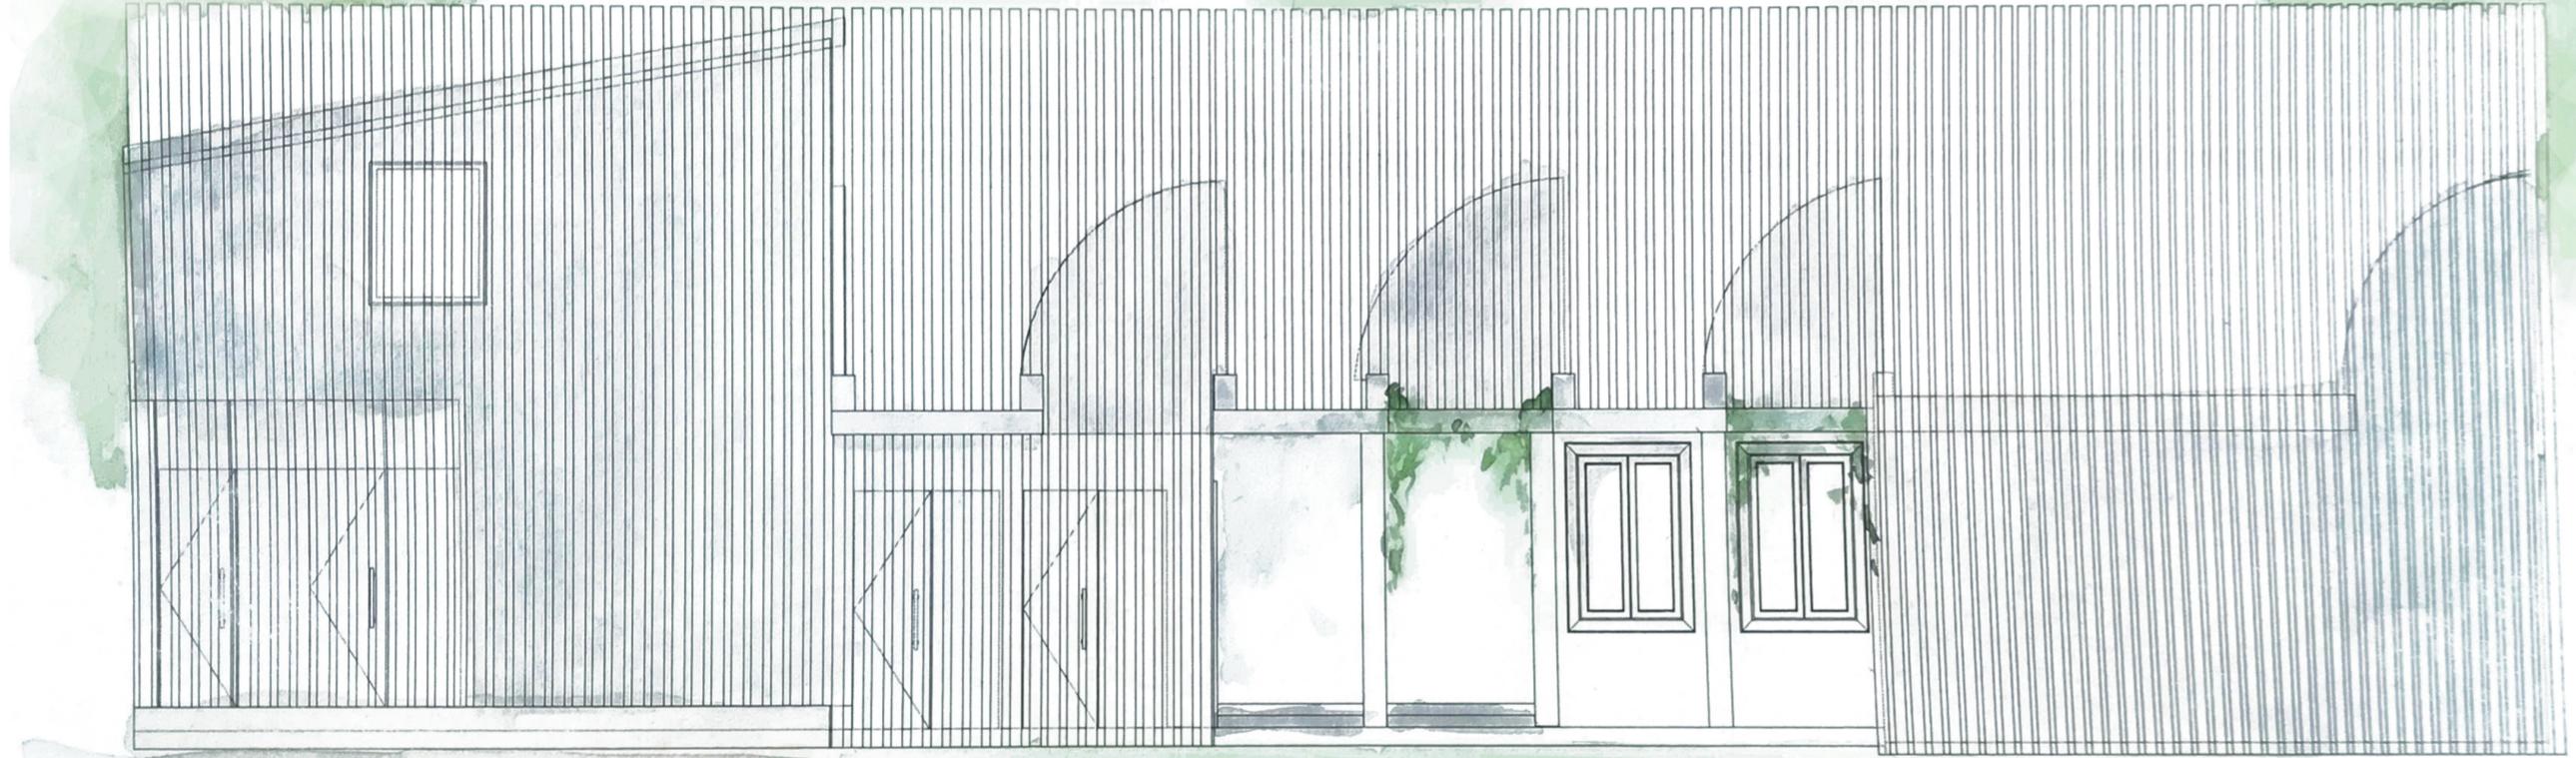


Prospetto realizzato con Revit e colorato con tecnica ad acquerello

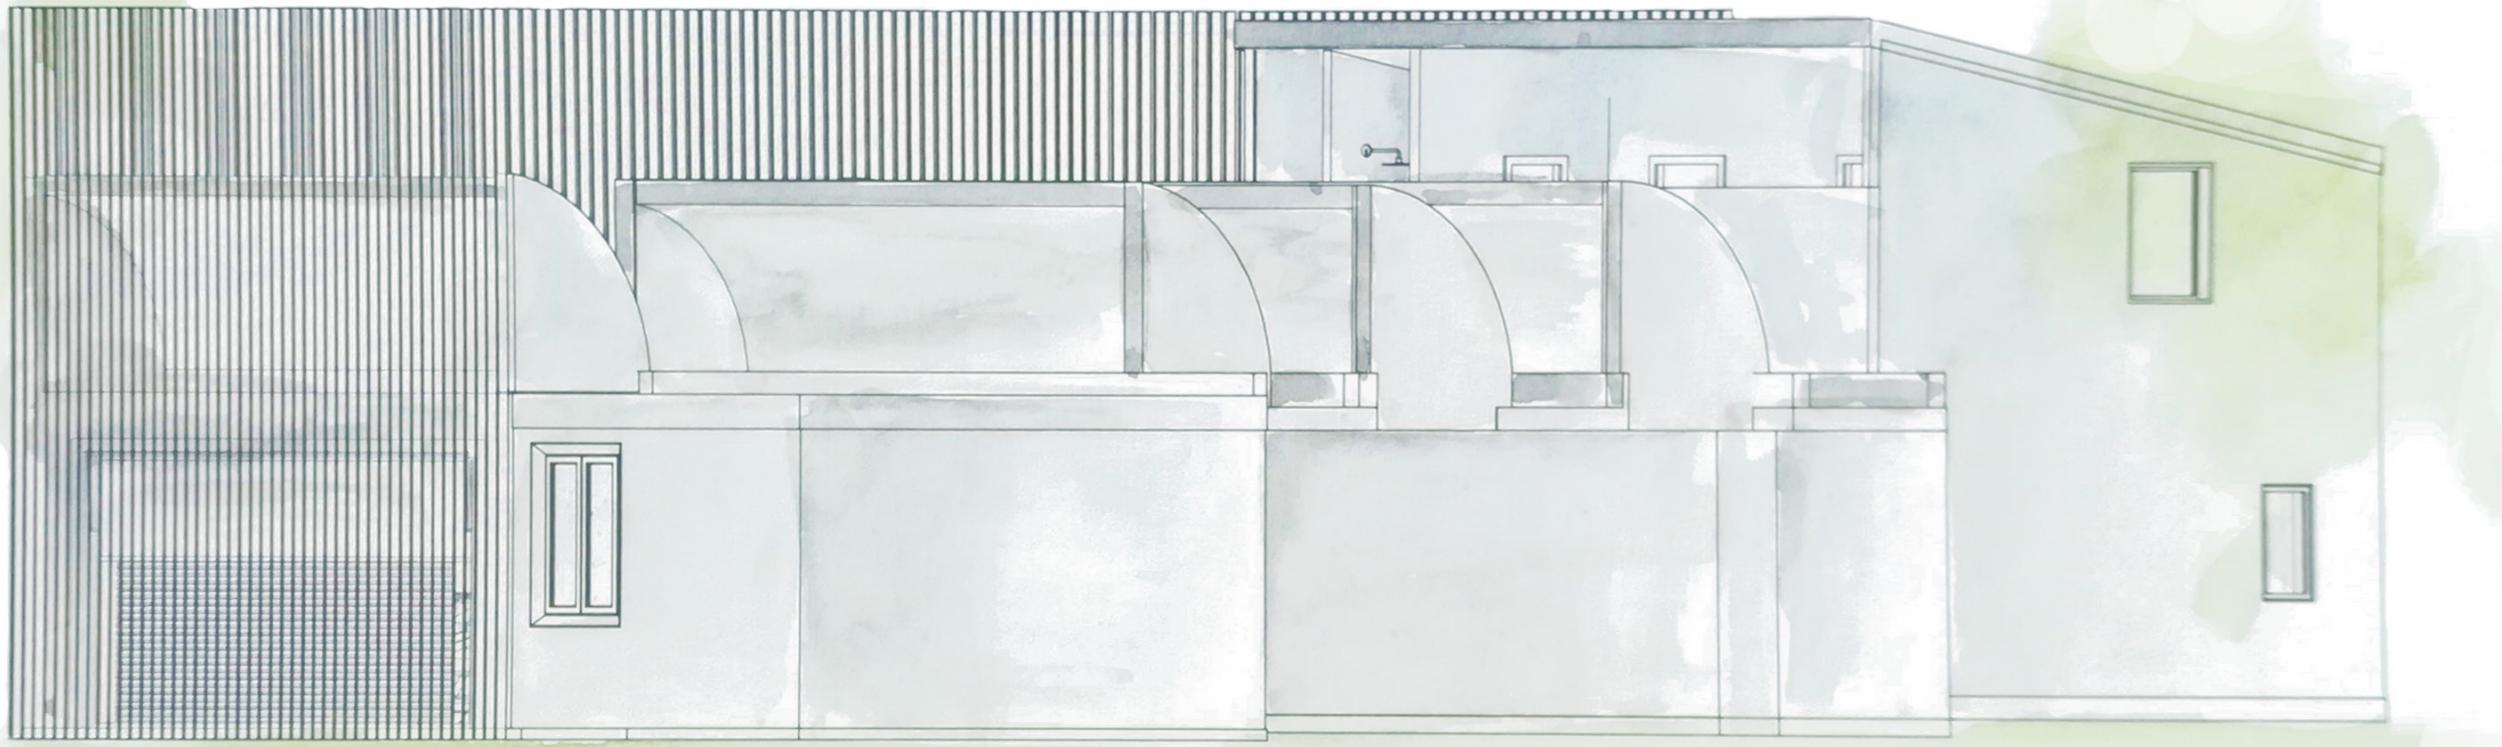

Vista tridimensionale realizzata con Revit e colorato con tecnica ad acquerello

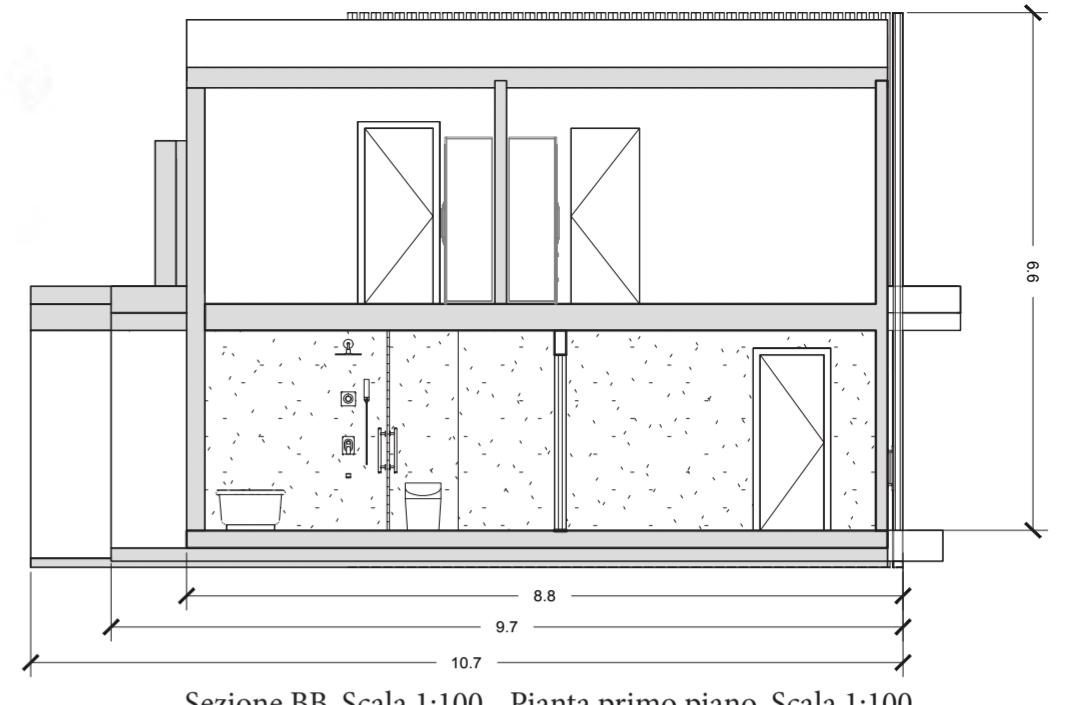


Sezione BB. Scala 1:100 Pianta primo piano. Scala 1:100

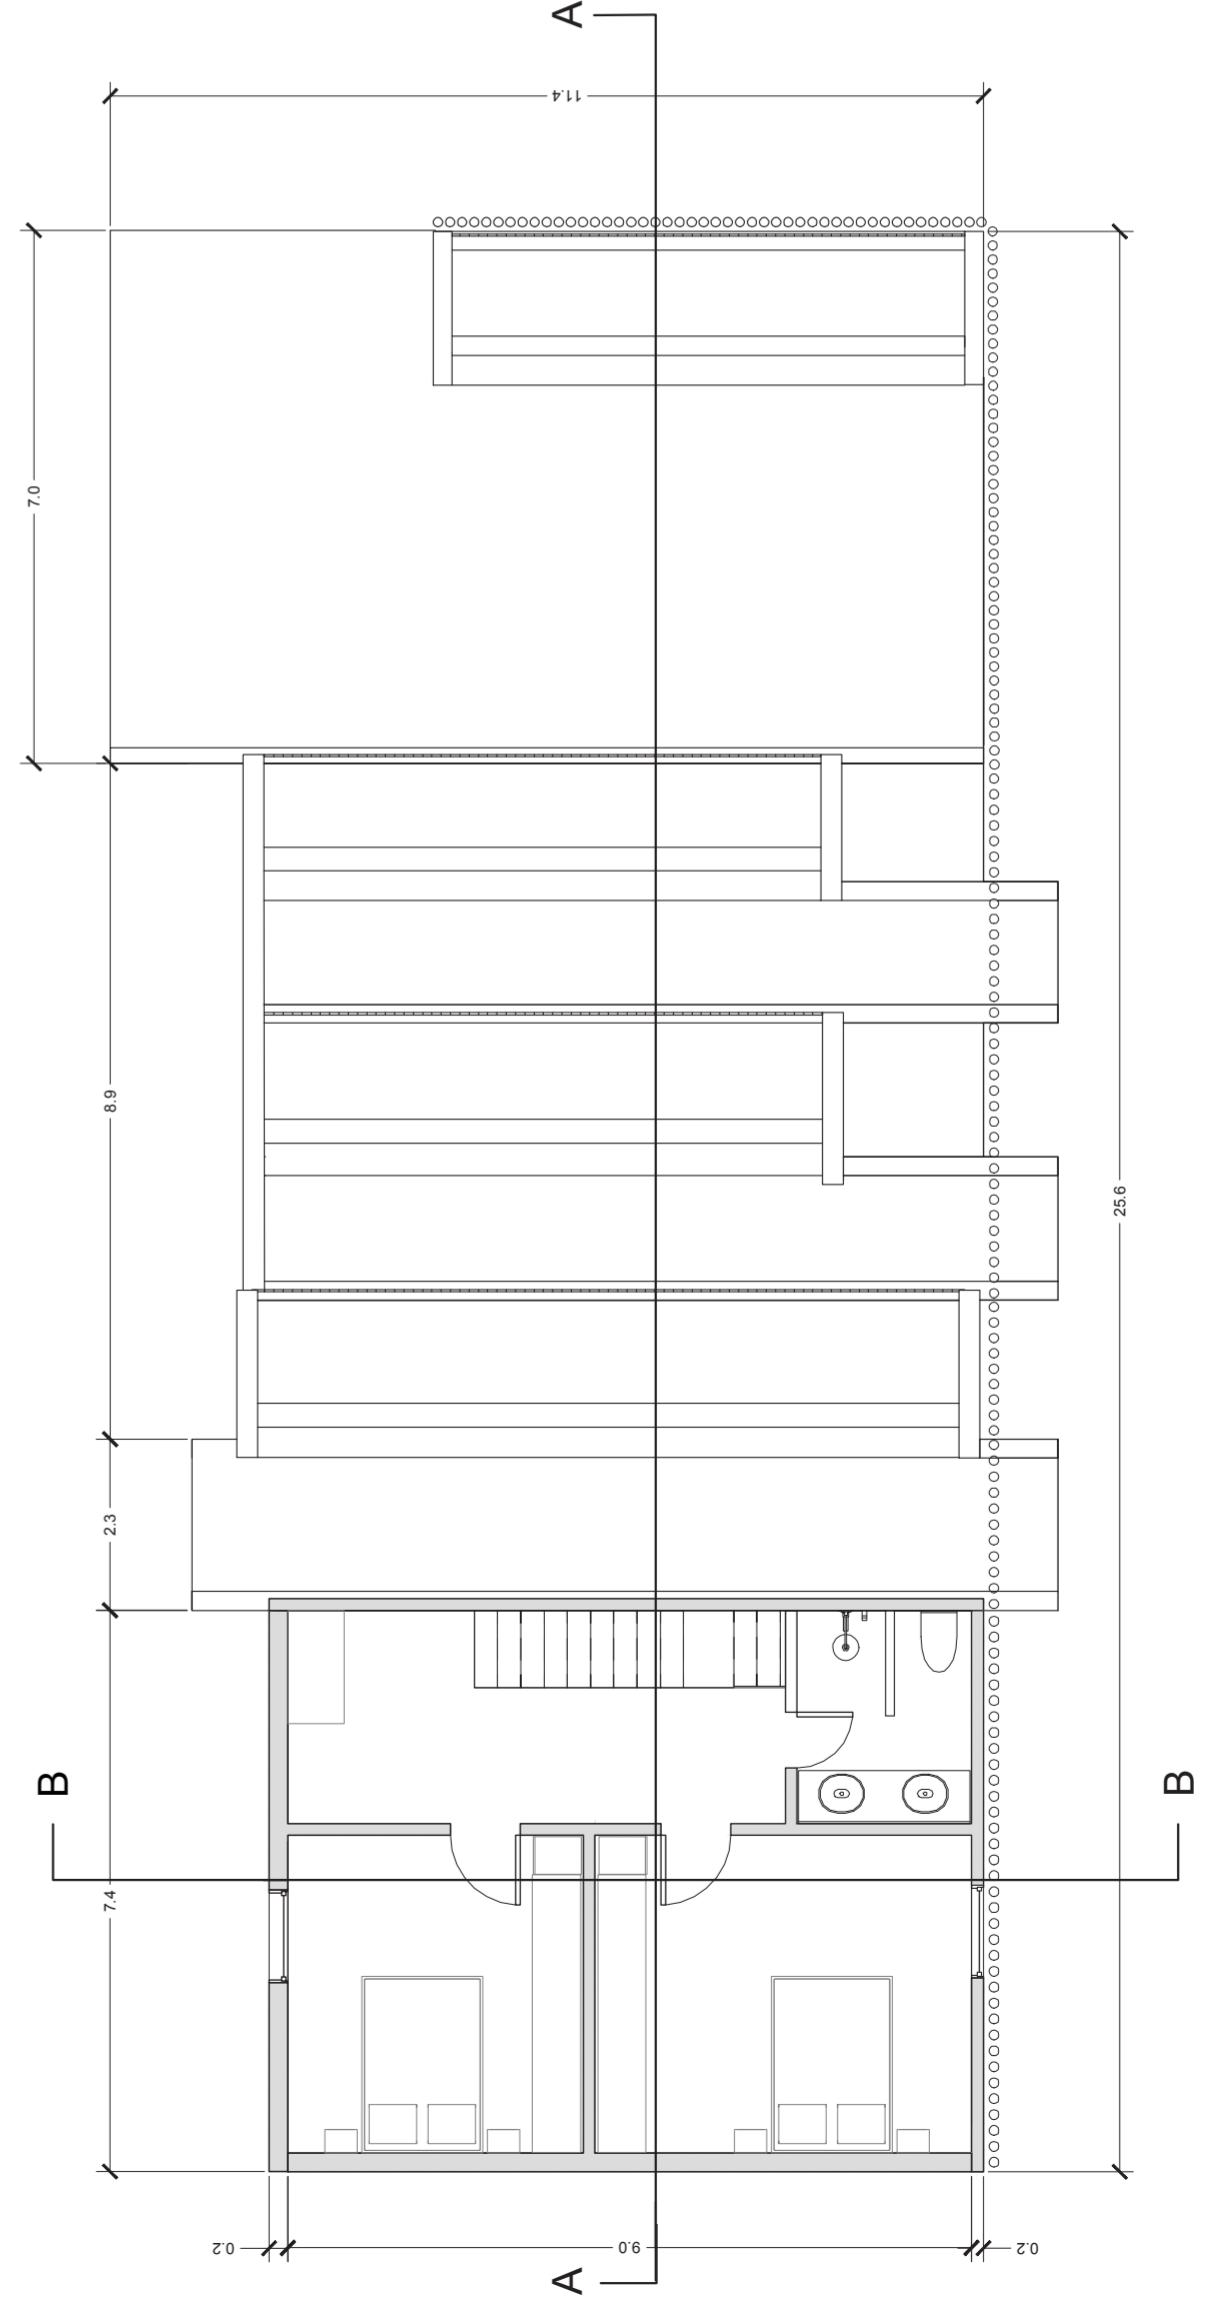



In basso a sinistra: Vista tridimensionale stampata con Revit e colorata con tecnica ad acquerello. Dettaglio privo di pilastri

Al centro: Vista tridimensionale stampata con Revit e colorata con tecnica ad acquerello. Spot su porta d'ingresso.



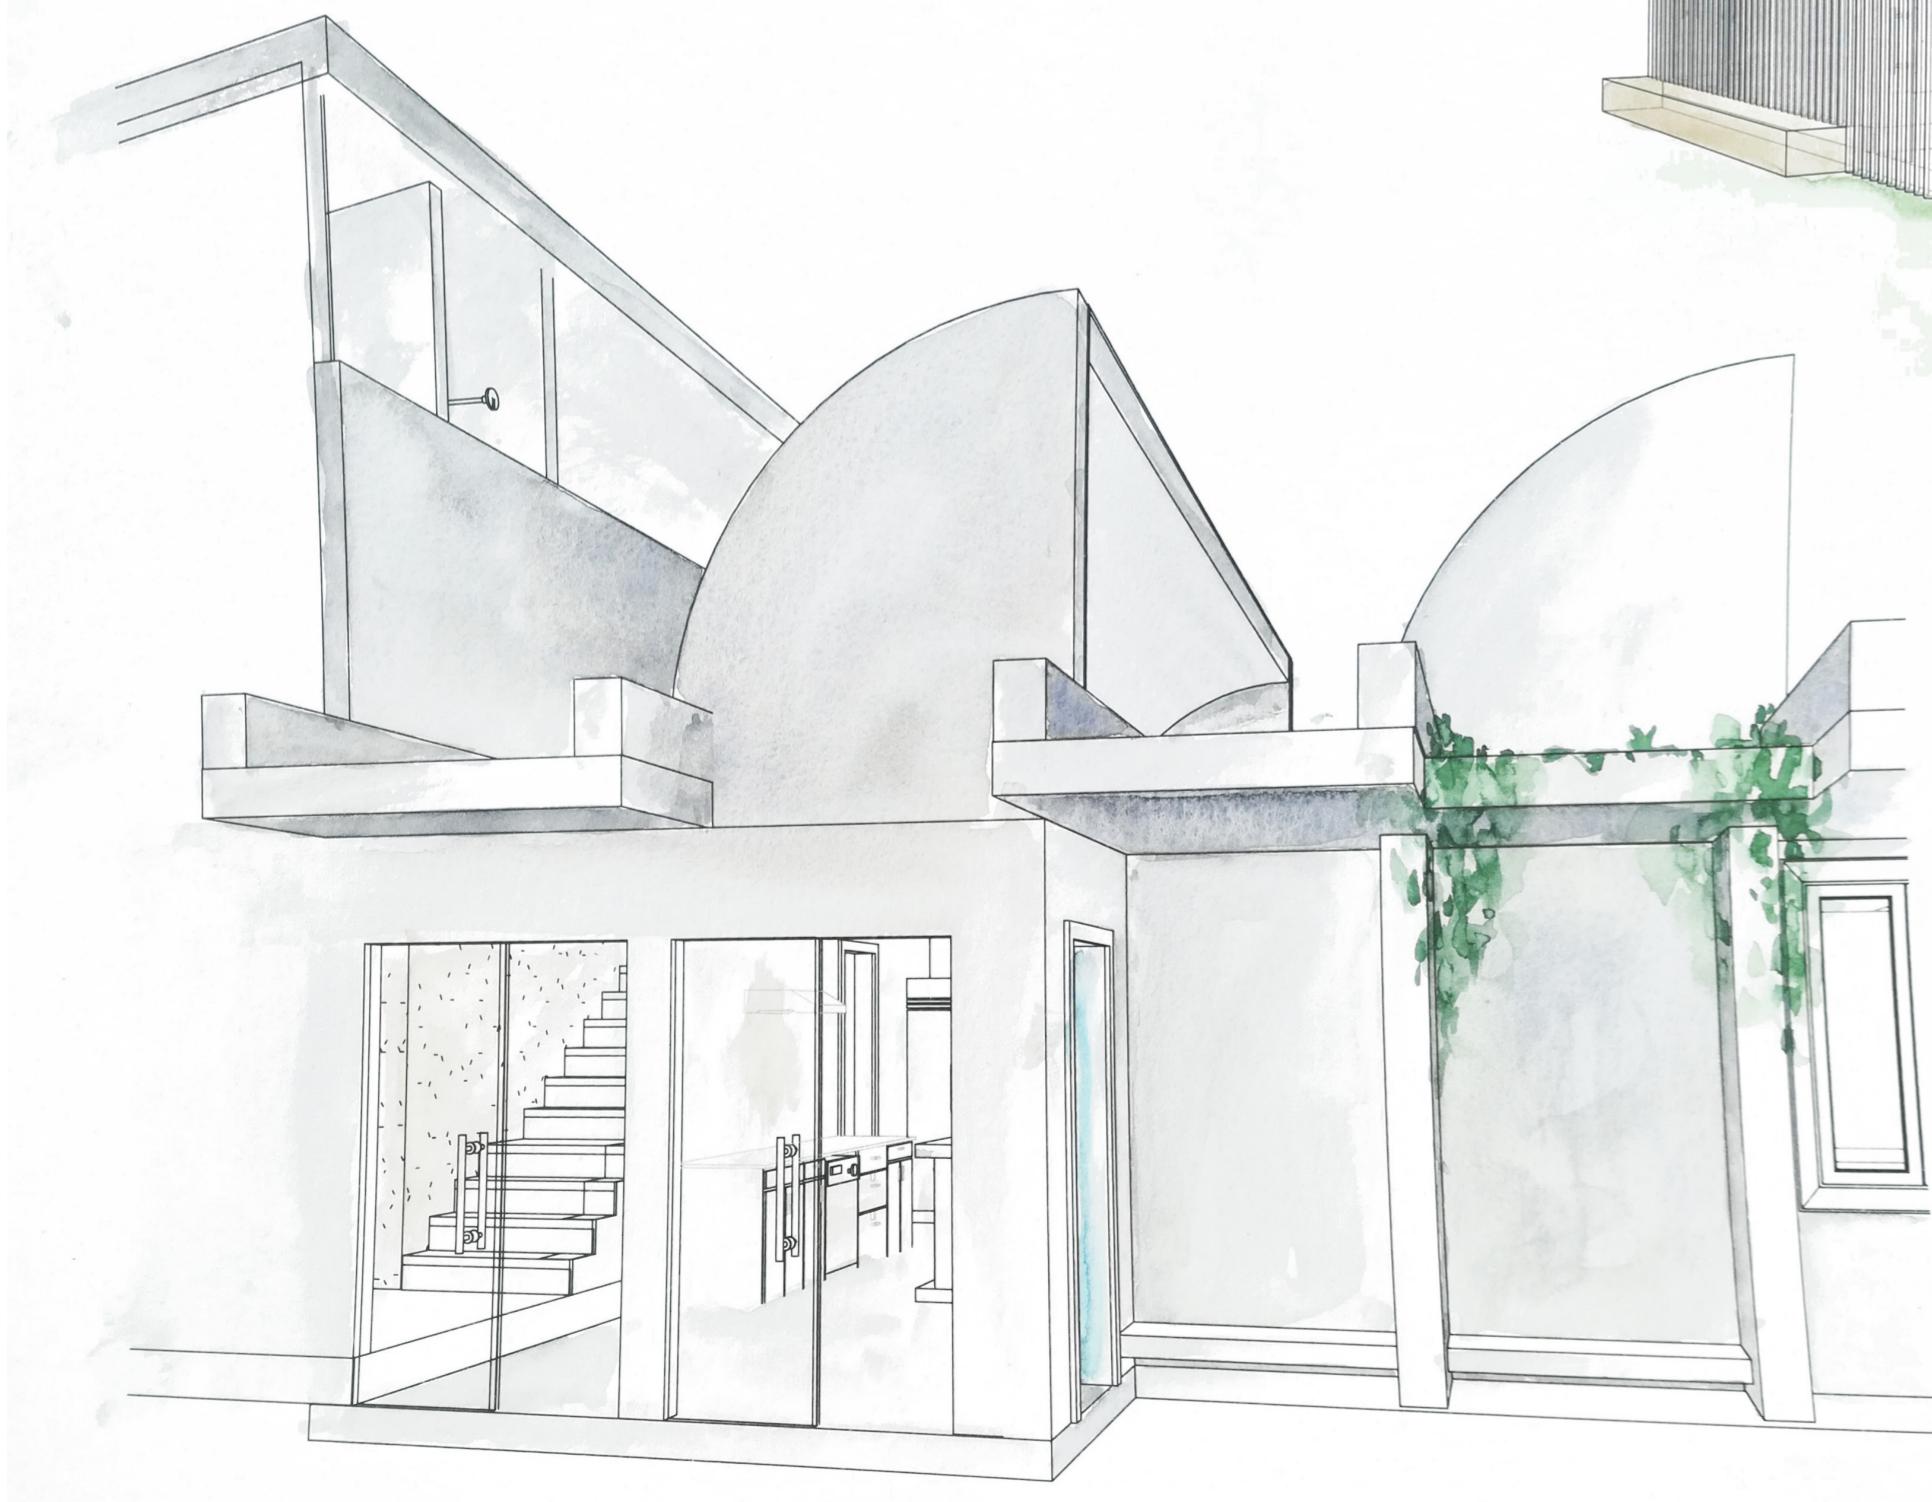


Le immagini illustrano alcune viste e dettagli dell'architettura. Risulta particolarmente interessante la coesione e l'accostamento tra il verde dell'edera rampicante e il grigio industriale del cemento. Peculiare è la presenza della porta color verde acqua che conferisce un tocco di colore di spicco rispetto ai toni complessivi dell'edificio.

In alto a destra: Foto della facciata principale


Al centro a destra: Foto di dettaglio della porta d'ingresso

In basso a destra: Foto di dettaglio di edera e cemento

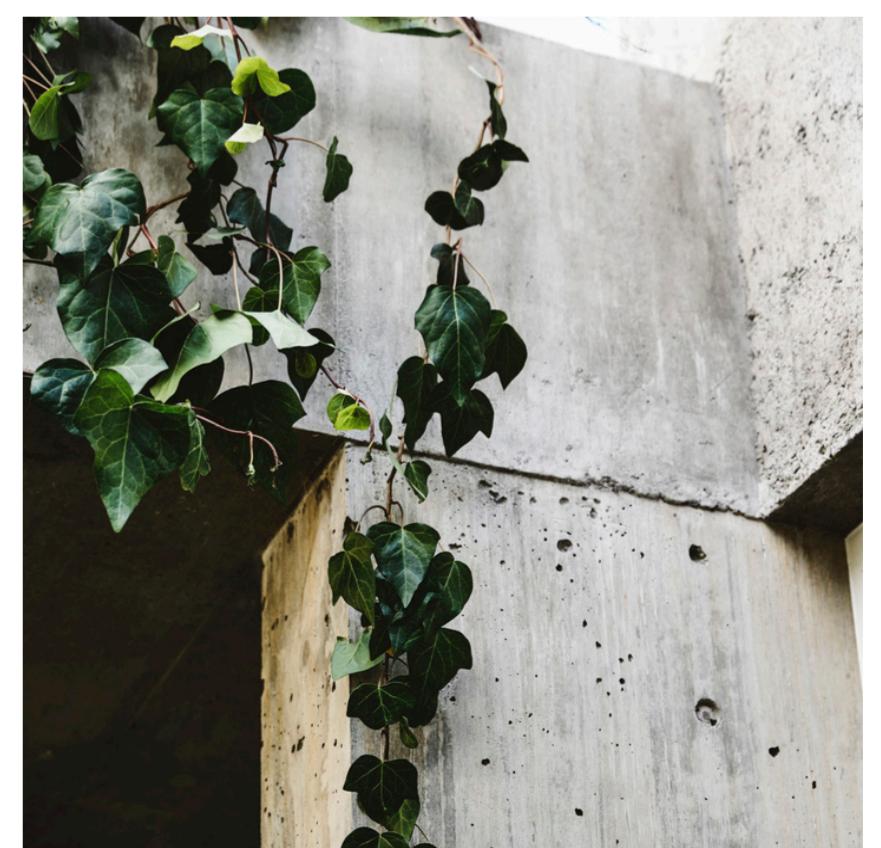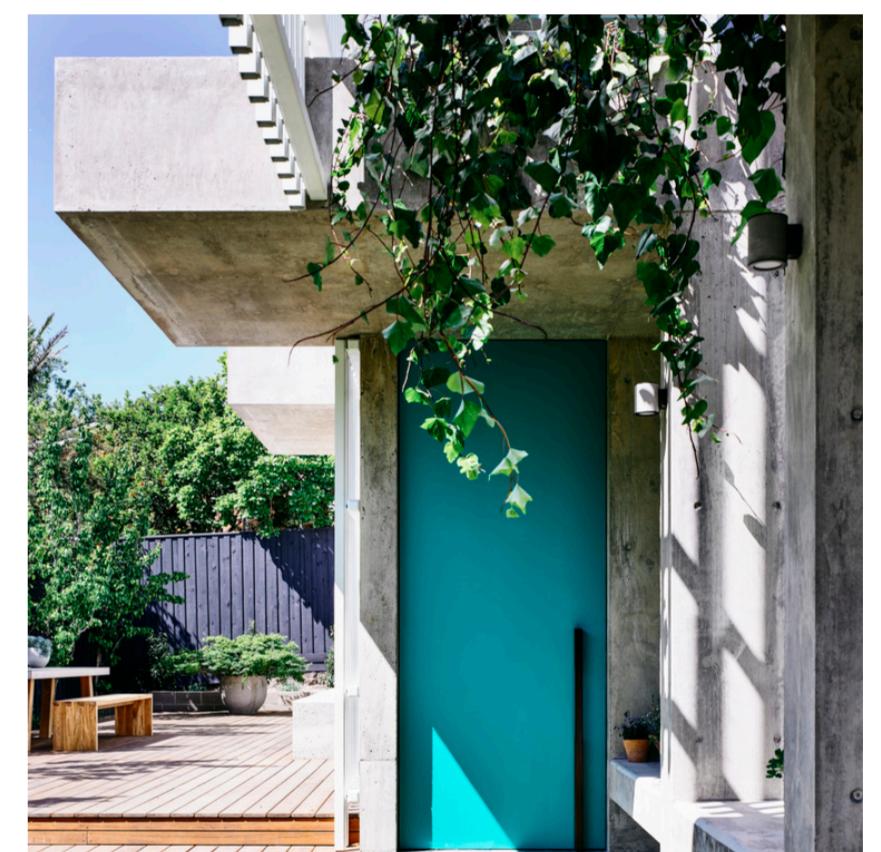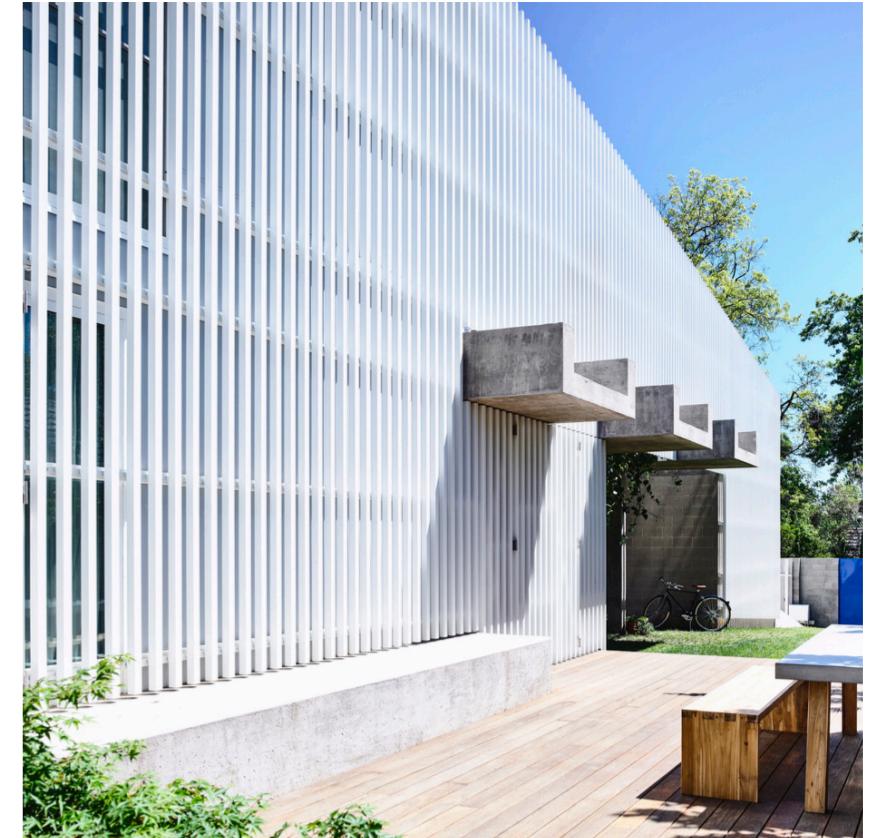



In basso a sinistra: Vista tridimensionale stampata con Revit.
Vista scale e cucina

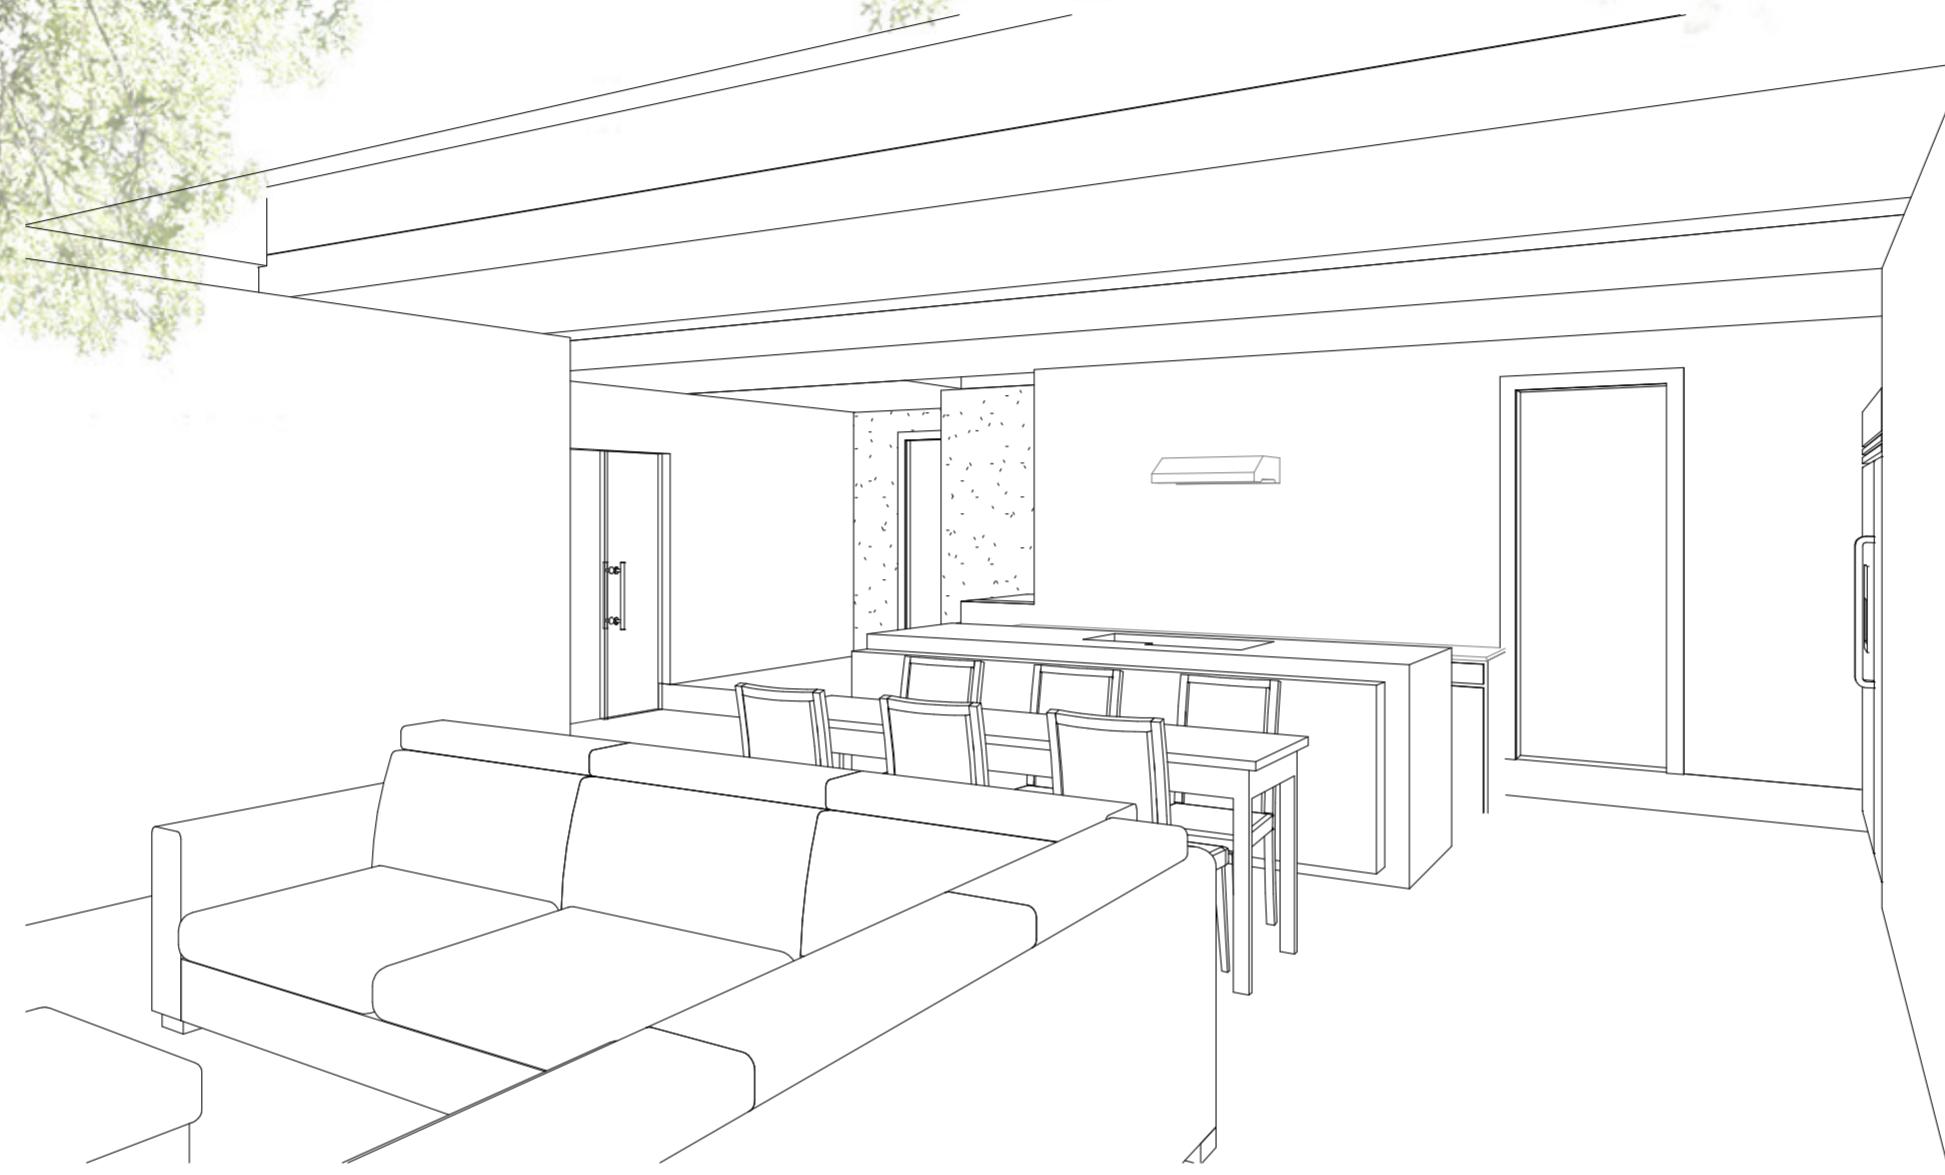

Al centro: Vista tridimensionale stampata con Revit.
Vista zona living e cucina



Le immagini illustrano alcune viste e dettagli degli interni dell'architettura. Come è possibile notare grande spazio viene dedicato alla zona living, centro e fulcro della residenza. Proprio a questa zona è stata infatti rivolta particolare attenzione in relazione all'illuminazione, difatti le volte che costruiscono il soffitto illuminano interamente lo spazio

In alto a destra: Foto di uno dei bagni

Al centro a destra: Foto della zona living

In basso a destra: Foto della camera da letto

