

# GC HOUSE



Architetto: Juan Pablo Ribadeneira  
Mora

Luogo: Quito, Ecuador


Costruttore: Jose Ponce Gonzalez

Anno: 2016

Area: 420 m<sup>2</sup>

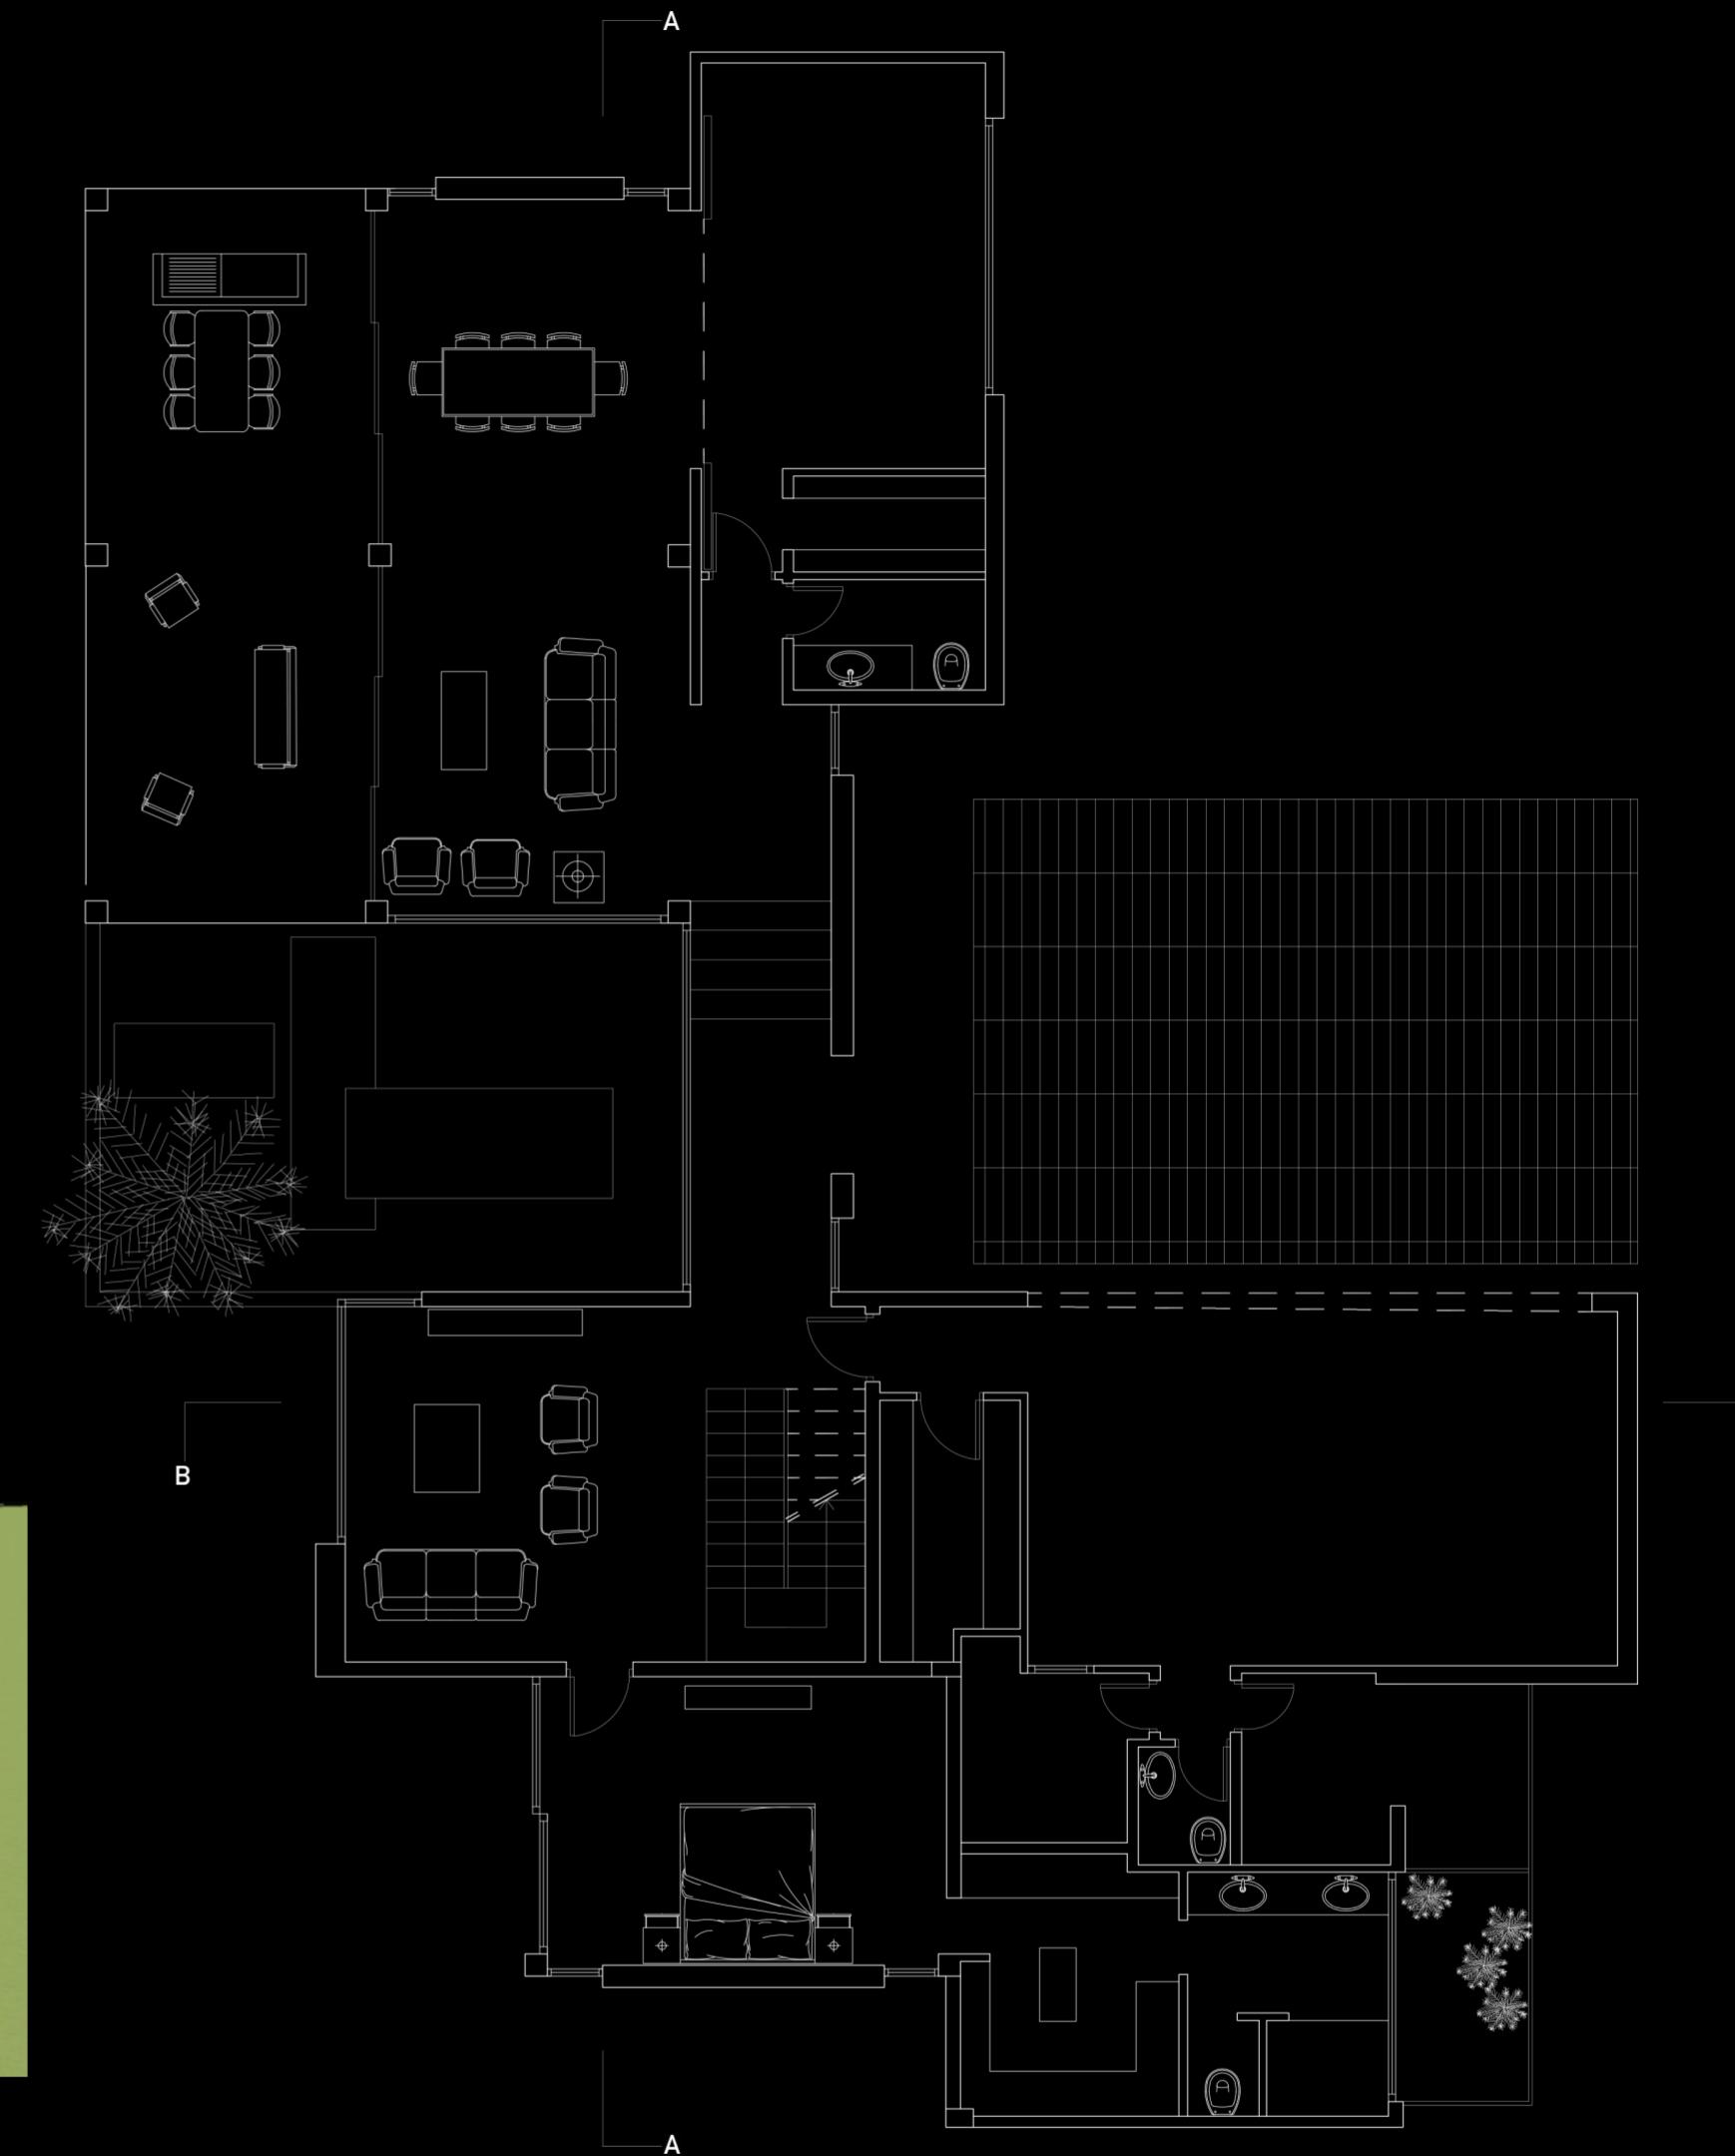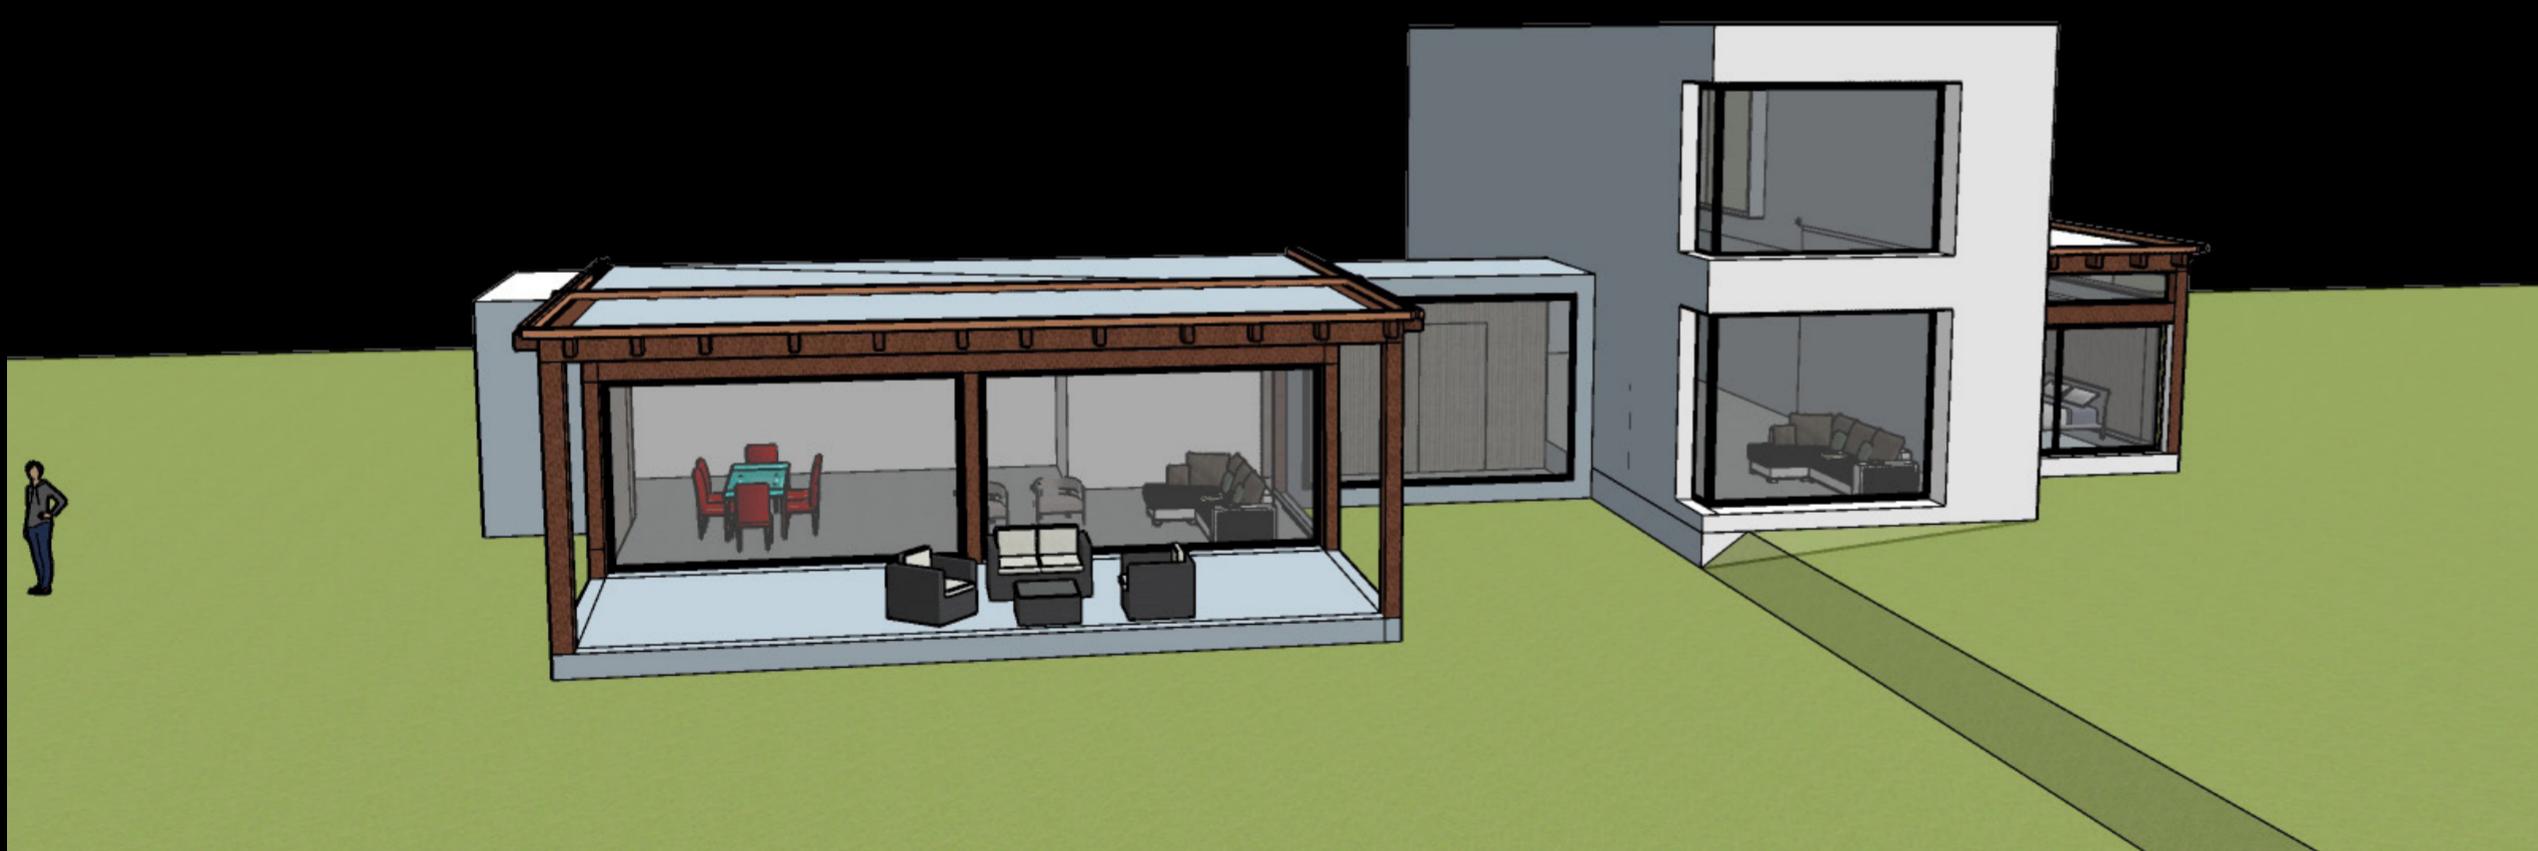

Pianta piano terra scala 1:100

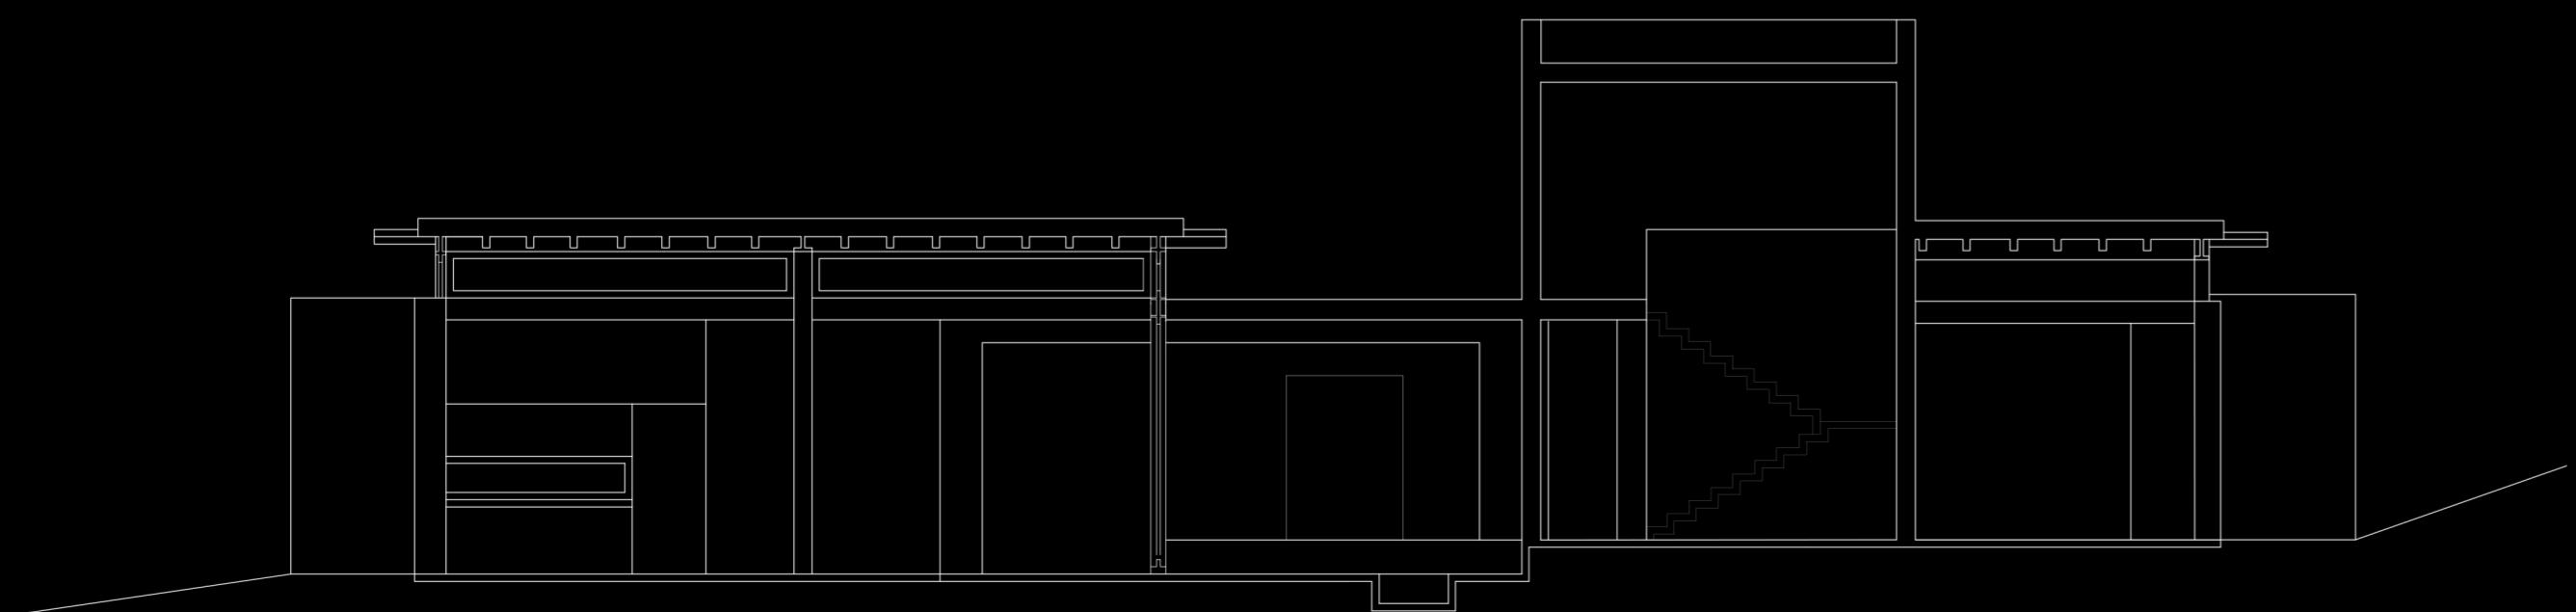


Sezione A-A




La GC House si trova nelle valli circostanti di Quito, in Ecuador. La casa è stata appositamente progettata e orientata nord-sud, aprendosi verso il lato meridionale, proteggendo dal sole i suoi lati orientali e occidentali, perché il sole è particolarmente forte in quanto il sito si trova in alta quota e si trova vicino all'equatore. La facciata nord è molto solida in quanto il quartiere circostante non ha recinzioni. Al contrario, la facciata sud è molto aperta, incorporando la casa con il suo prato. A causa della grande estensione del lotto, la maggior parte degli spazi si trova al piano terra. Solo due camere da letto al secondo piano. La casa è divisa in due aree principali. Una parte più intima, dove si trovano le camere da letto e i bagni, e una zona meno privata, dove si trovano il salotto, la cucina e la sala da pranzo. Questi due sono collegati dall'ingresso principale che diventa un ponte tra tutti gli spazi abitativi. Infine, un cortile centrale diventa il punto centrale della casa.



Interno camera matrimoniale piano terra

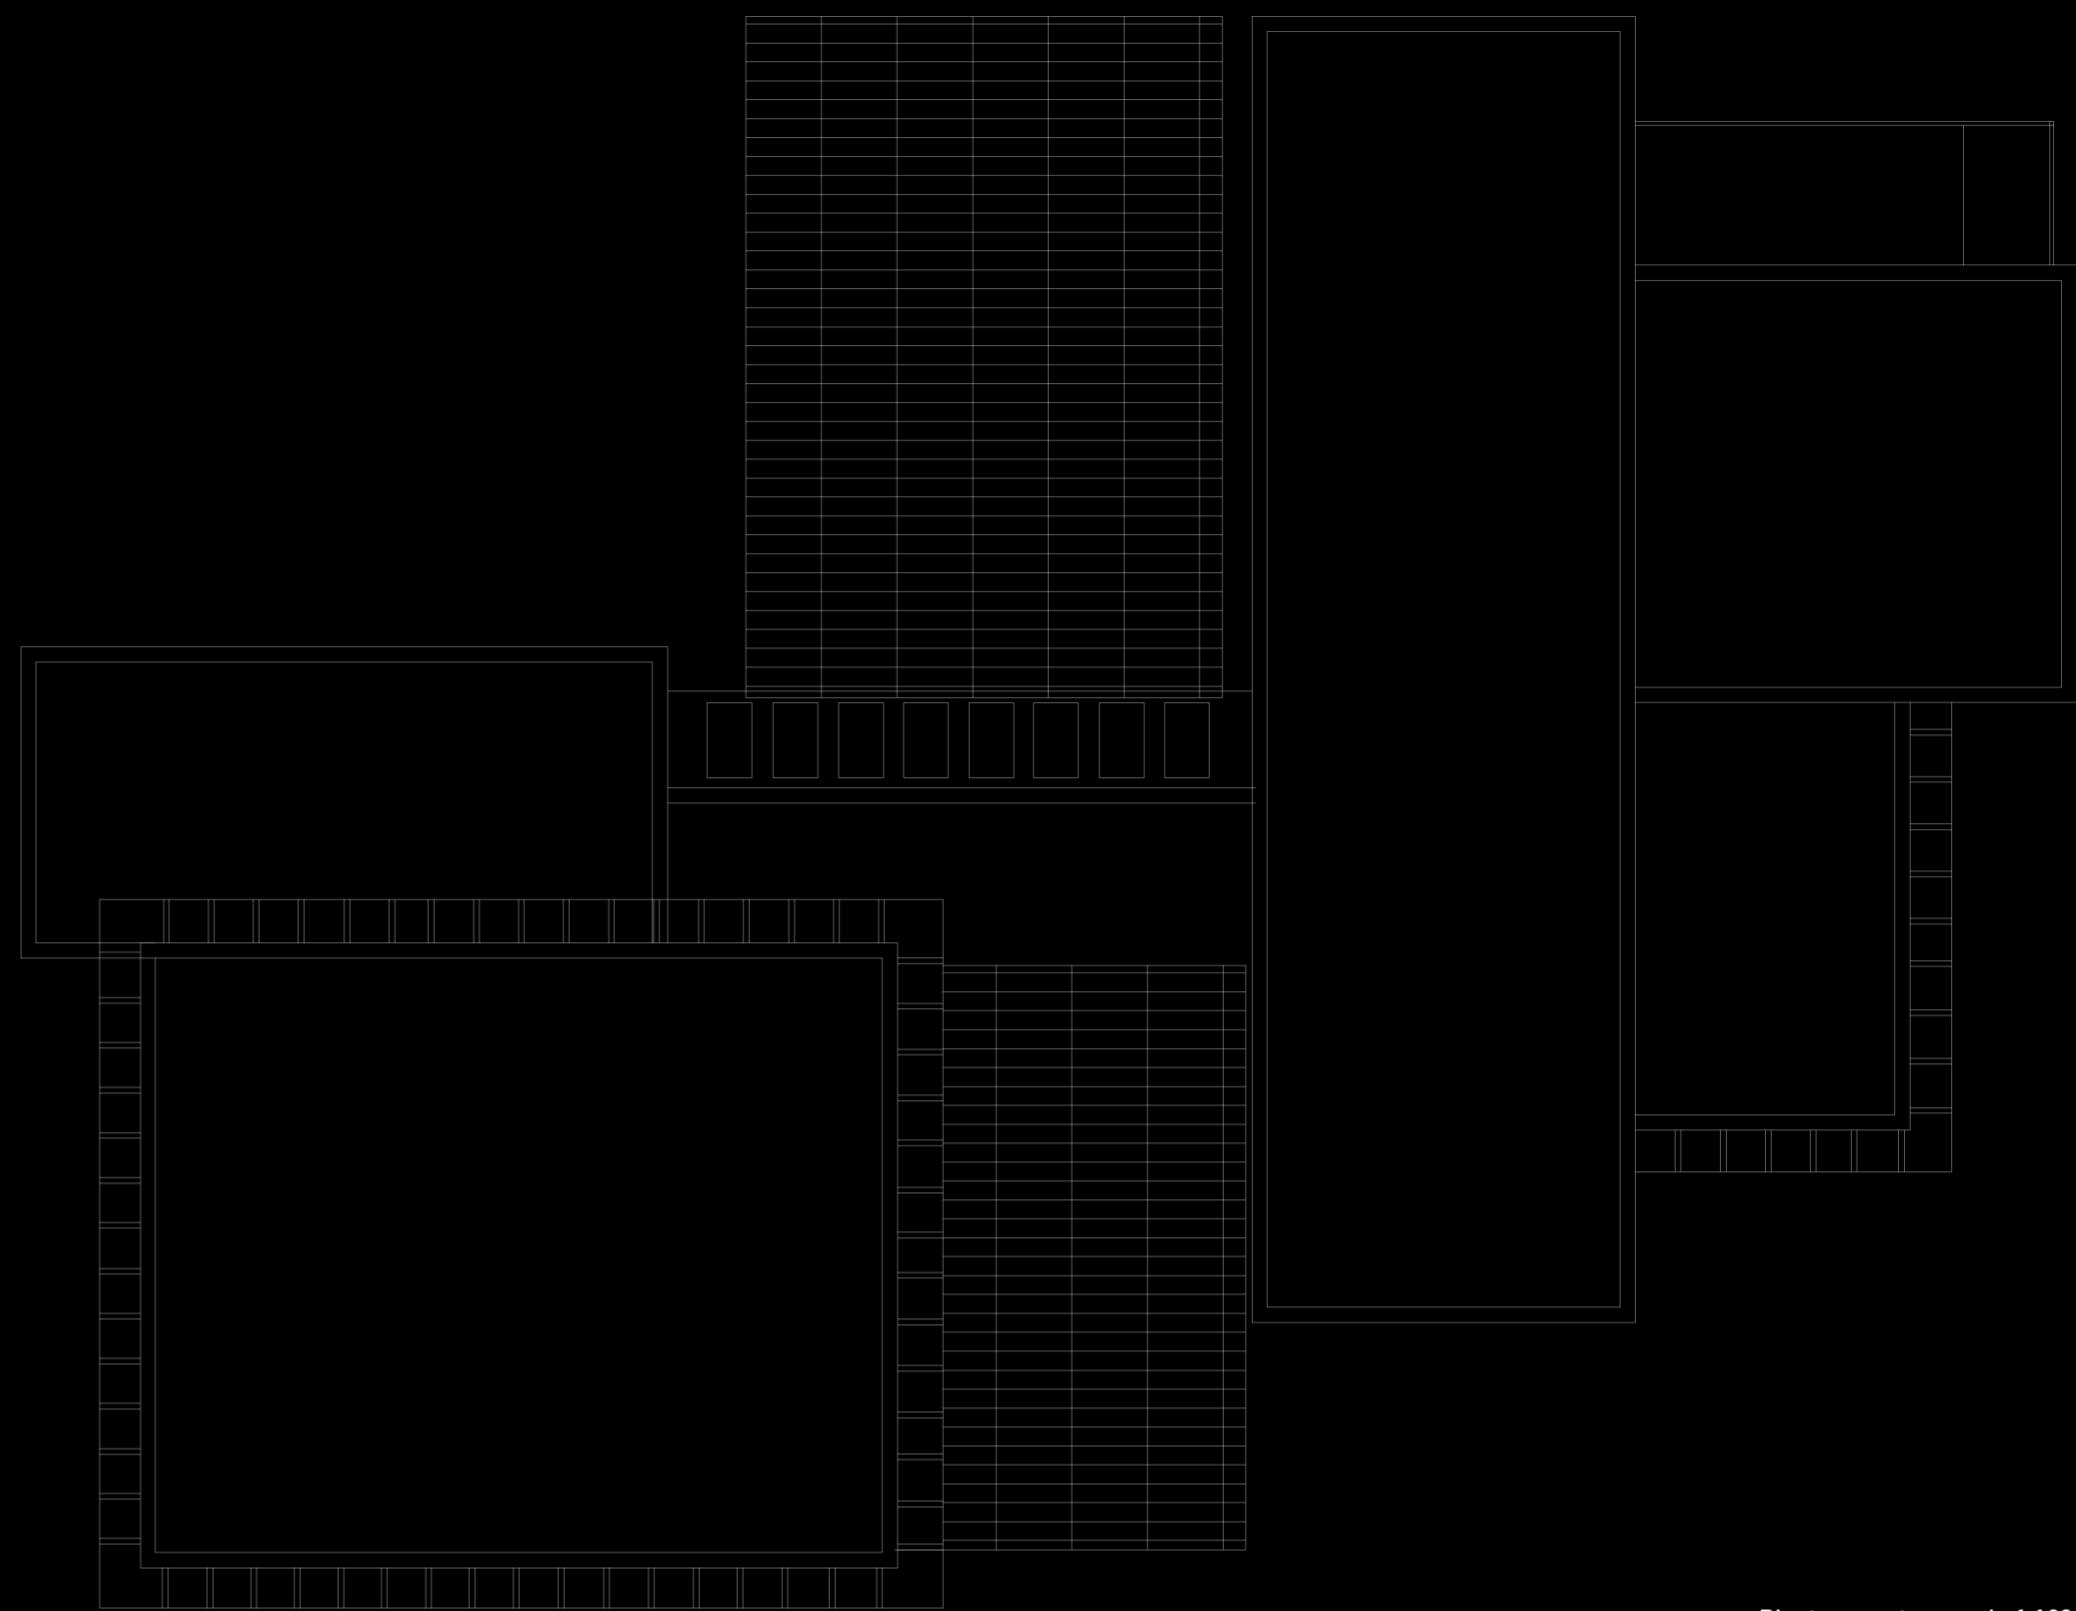

Pianta copertura scala 1:100

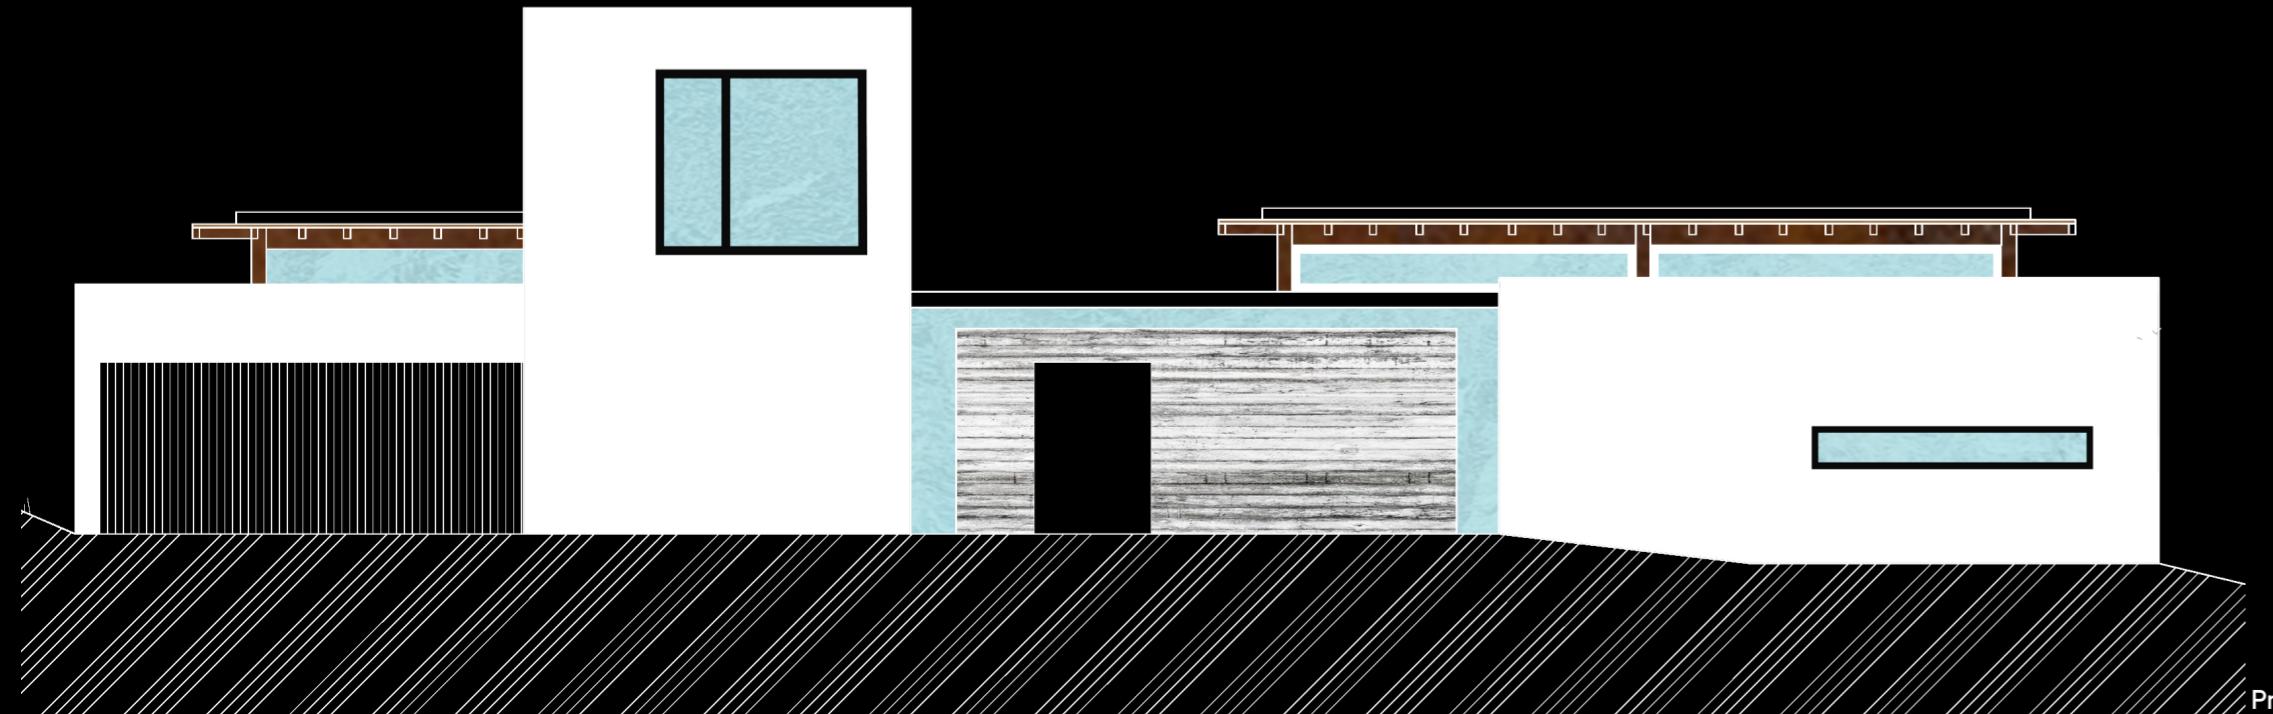

Prospetto frontale scala 1:100



Politecnico di Milano | Scuola del Design



Corso di laurea in Design Interni

Laboratorio di Strumenti e metodi del progetto | A.A.2017/2018 | Sez. I2


Docente: Marco Ferrara

Studenti: Daniele Bertelli (893345), Alessandro Leone(890840)



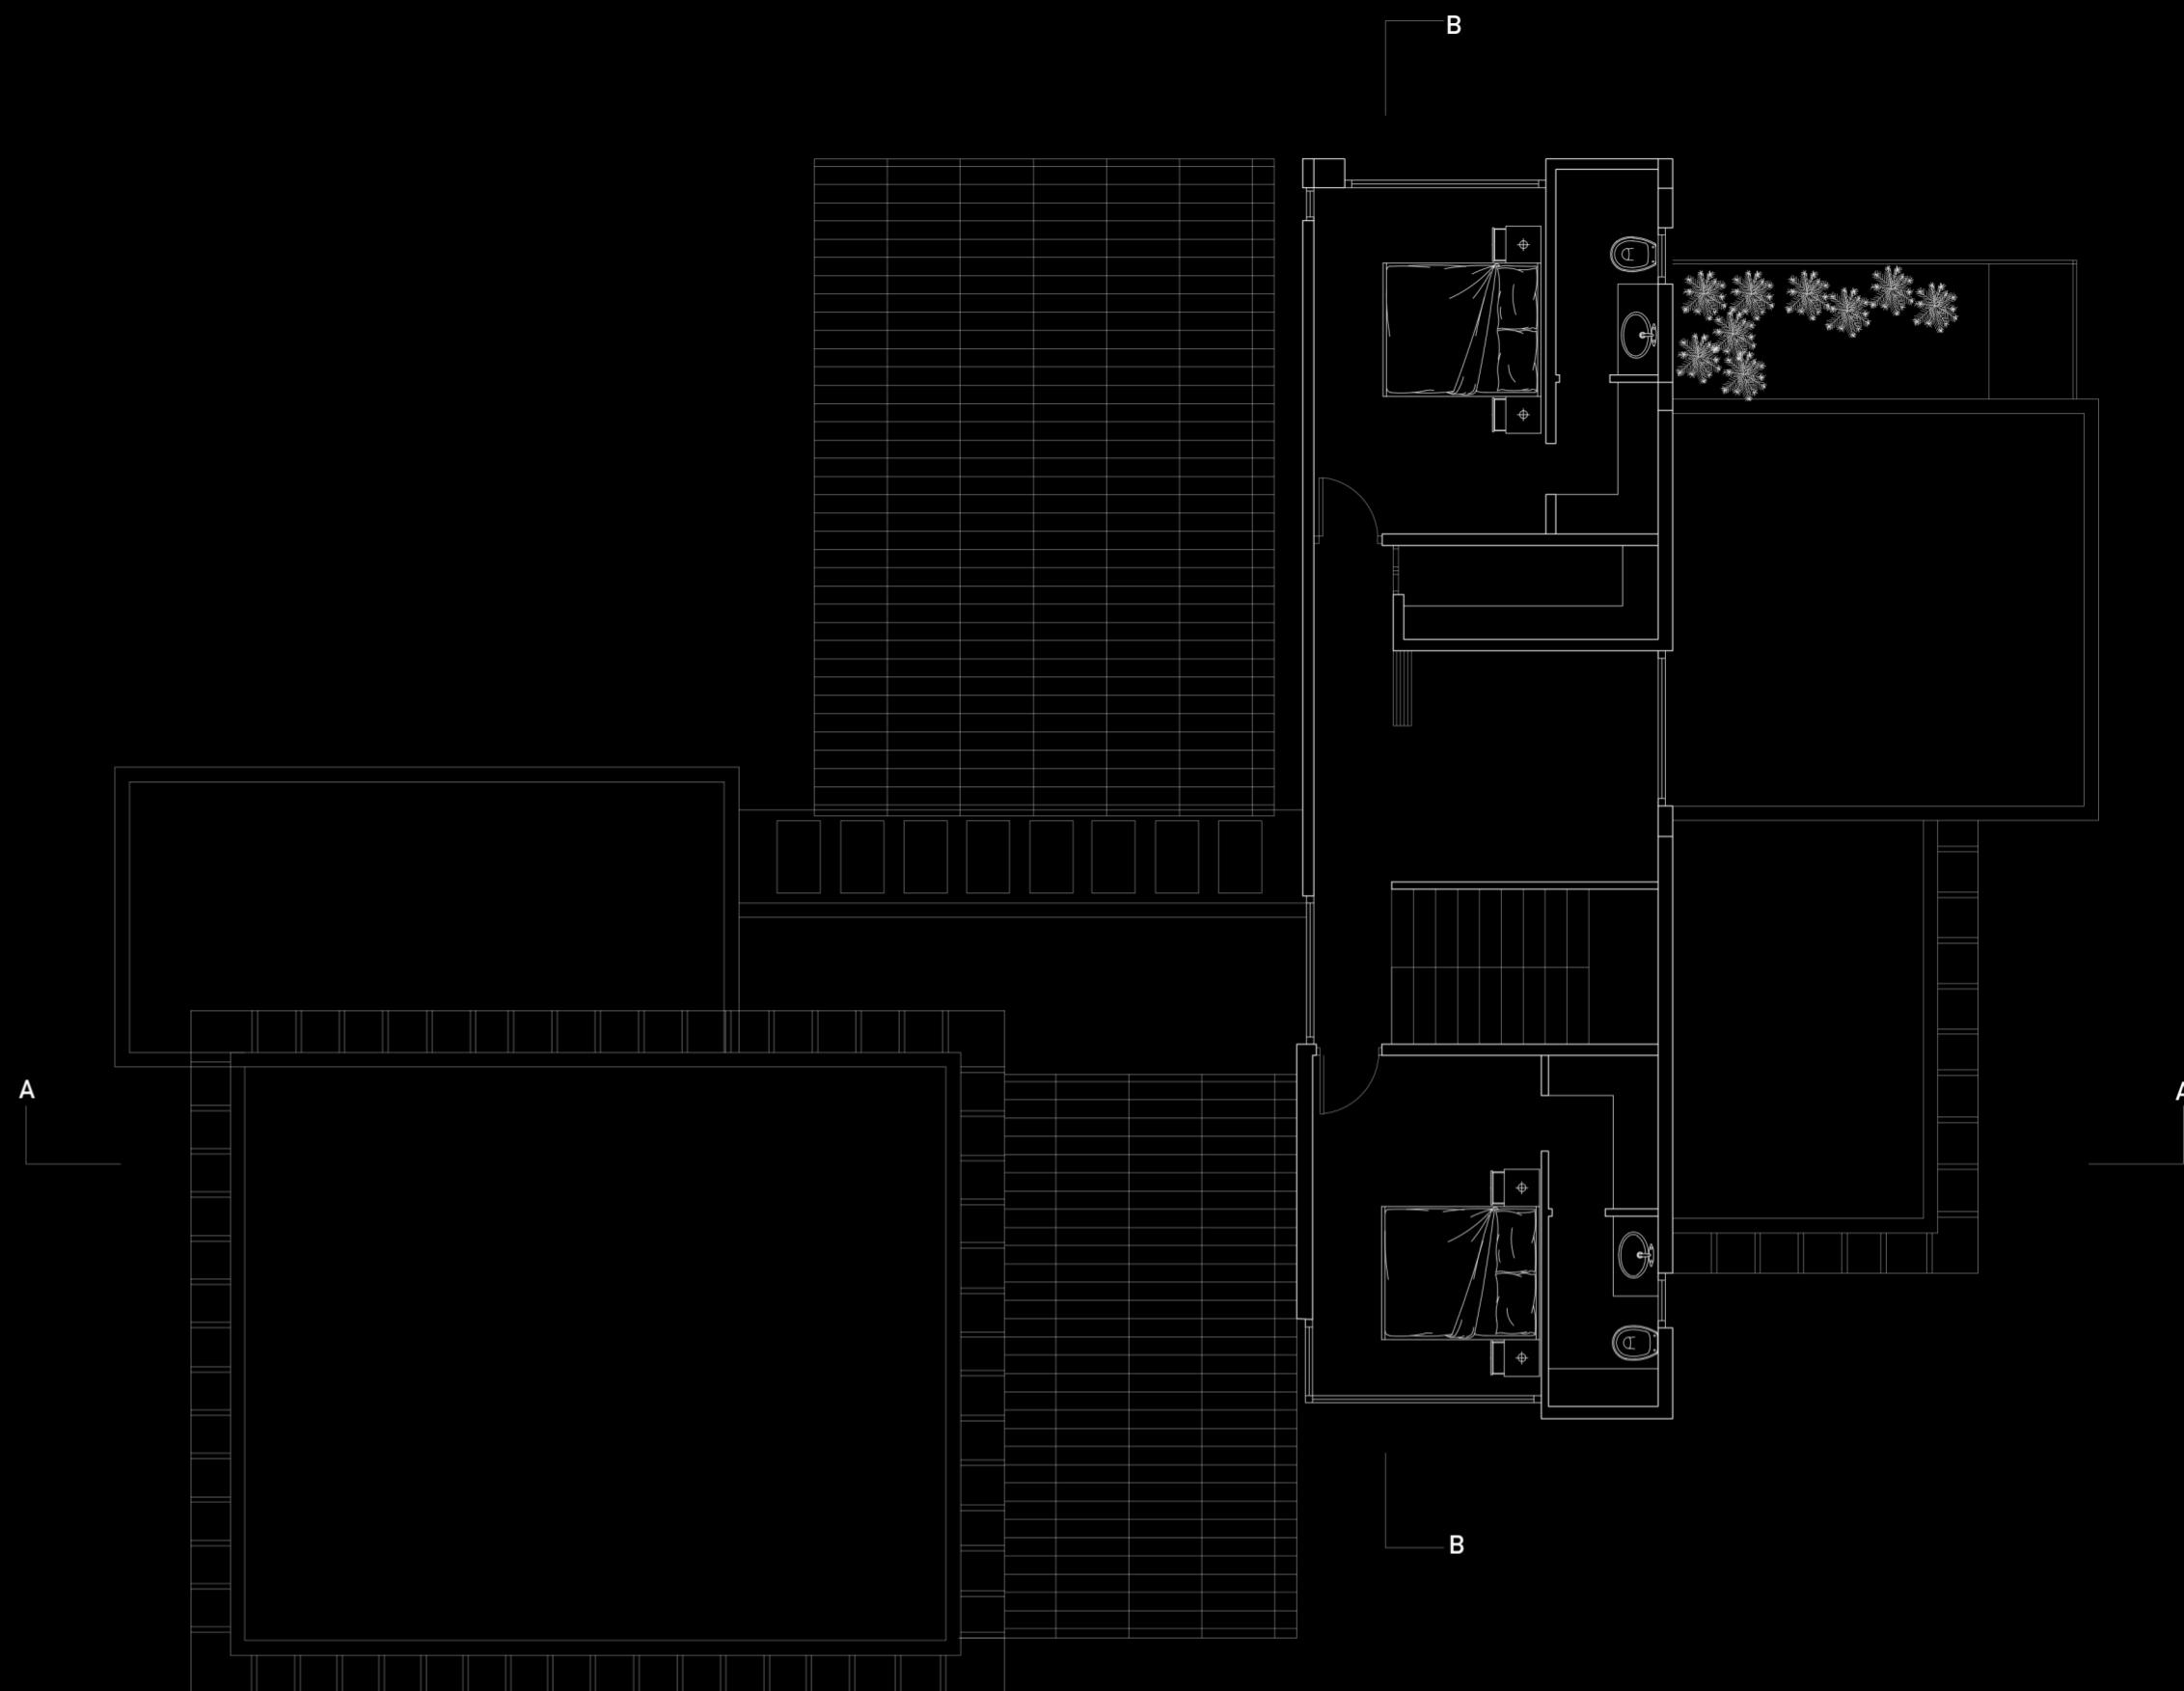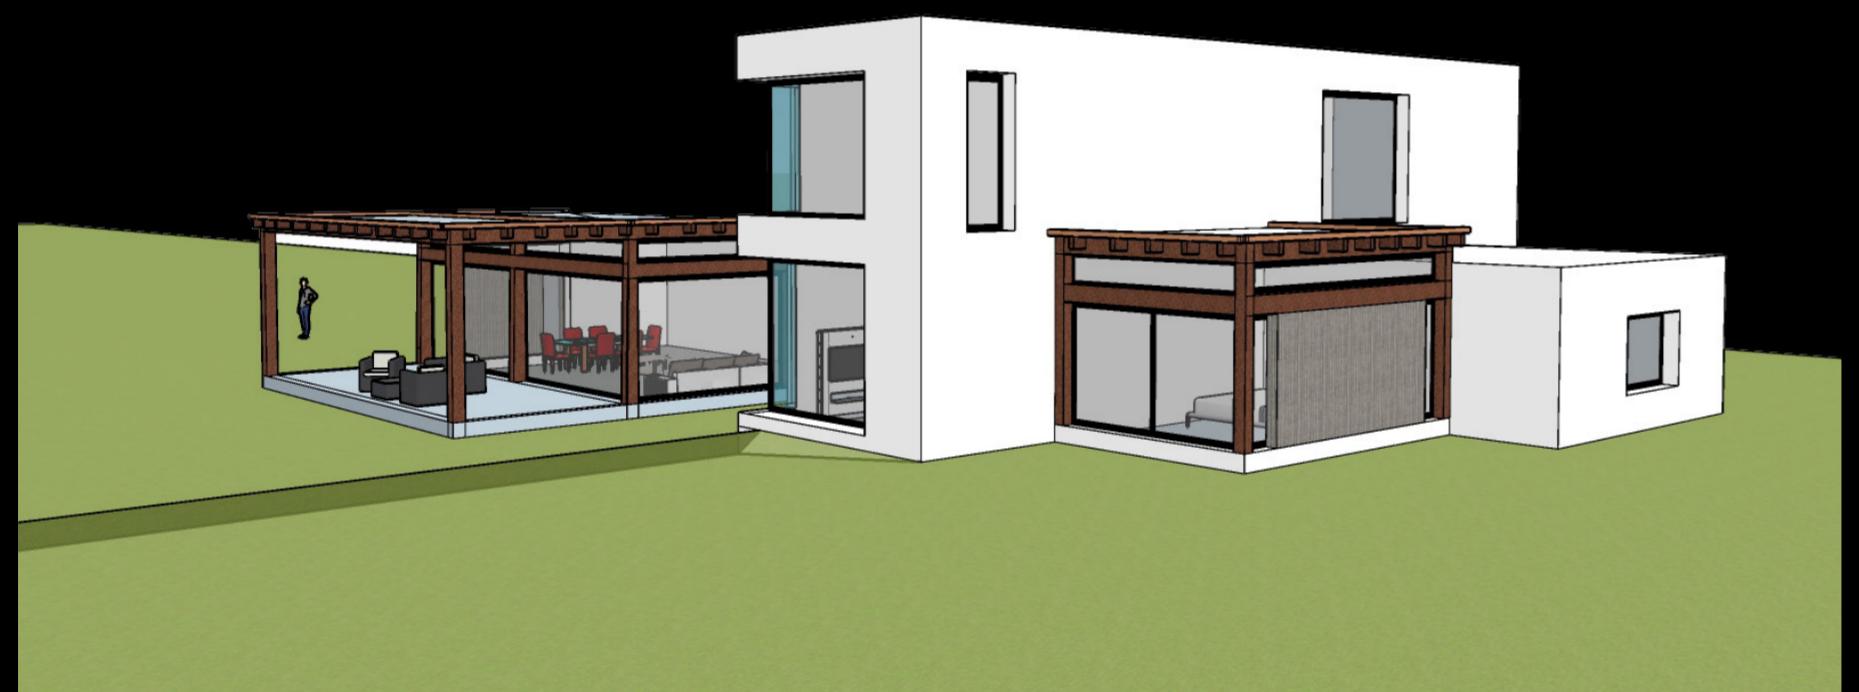

Pianta primo piano scala 1:100

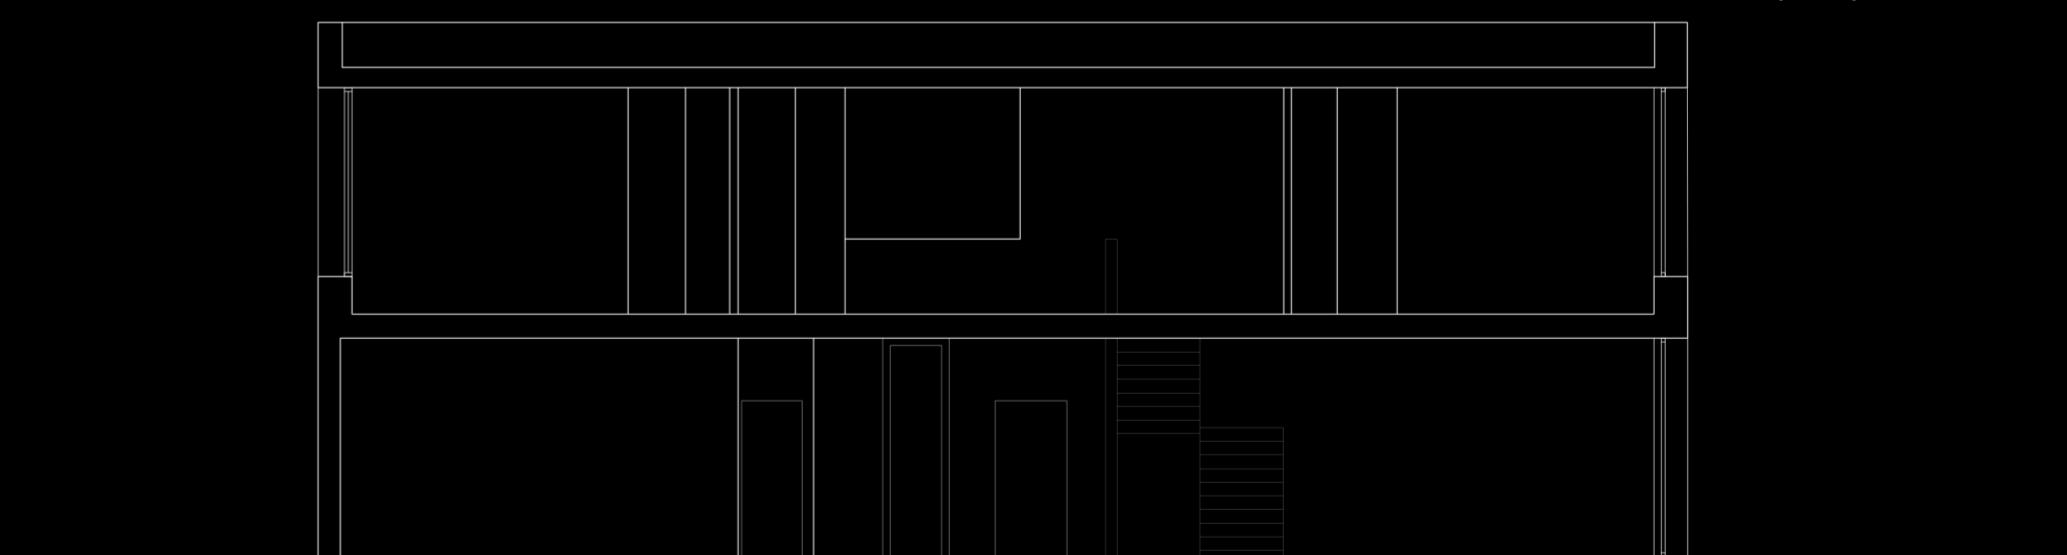

Sezione B-B scala 1:100

Prospetto posteriore scala 1:100

