

HOUSE IN KOBE



ARCHITECTS: FujiwaraMuro Architects

LOCATION: Japan

LEAD ARCHITECTS: Shintaro Fujiwara, Yoshio Muro

AREA: 97 mq


PROJECT YEAR: 2014

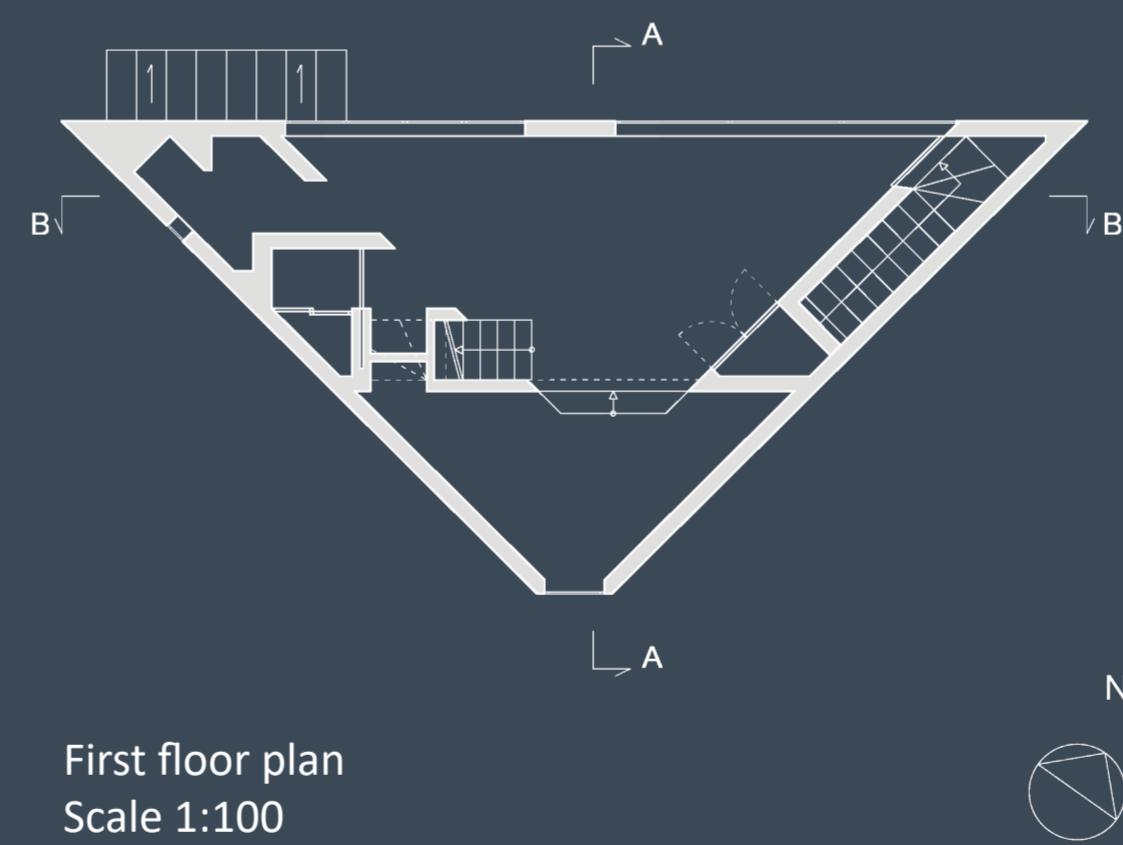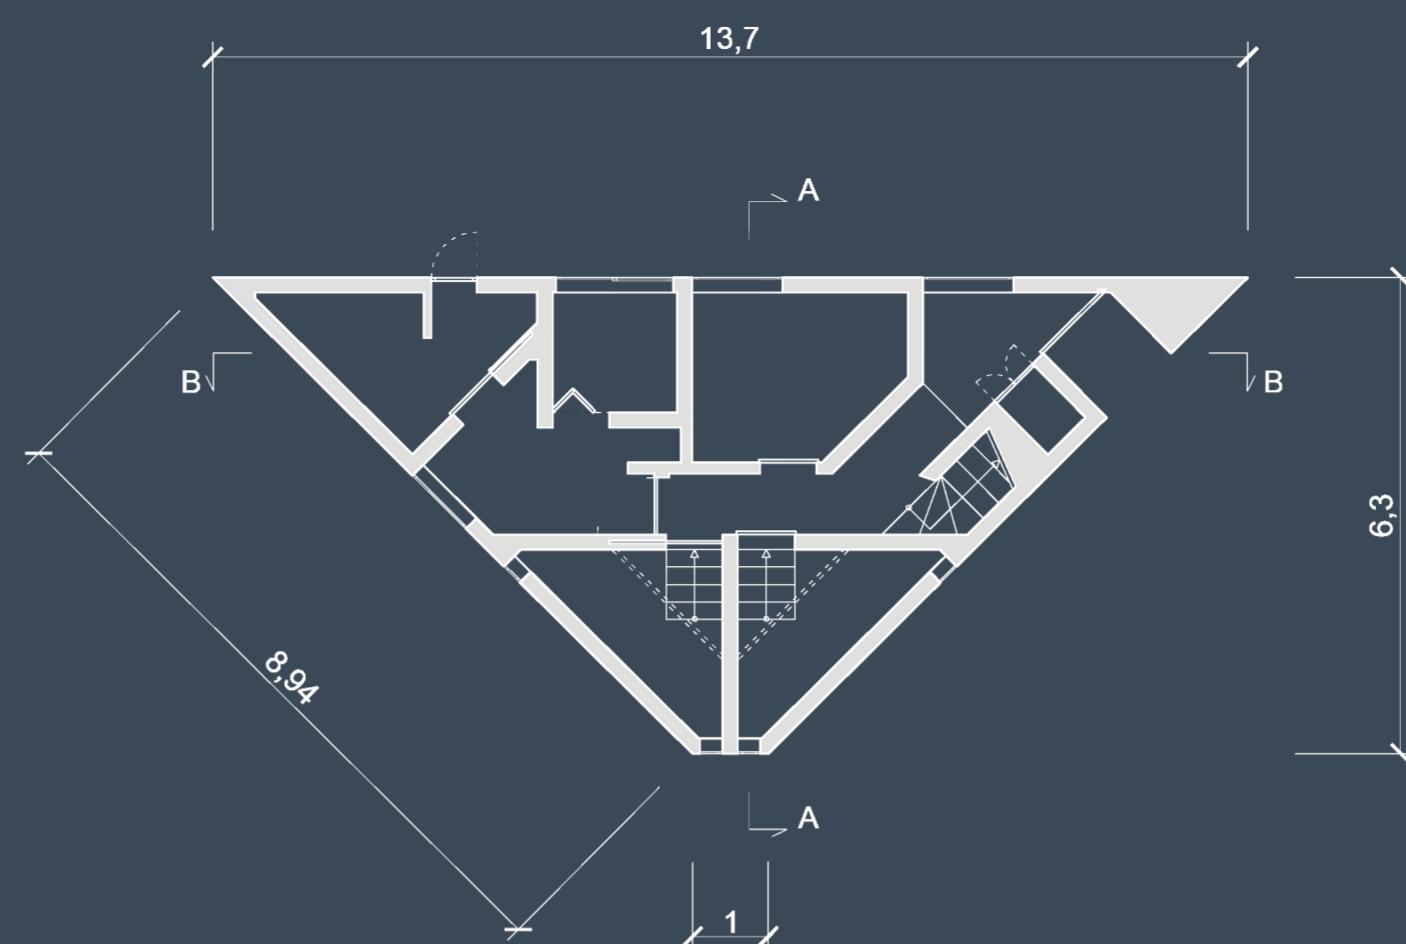


South-east elevation



North-west elevation

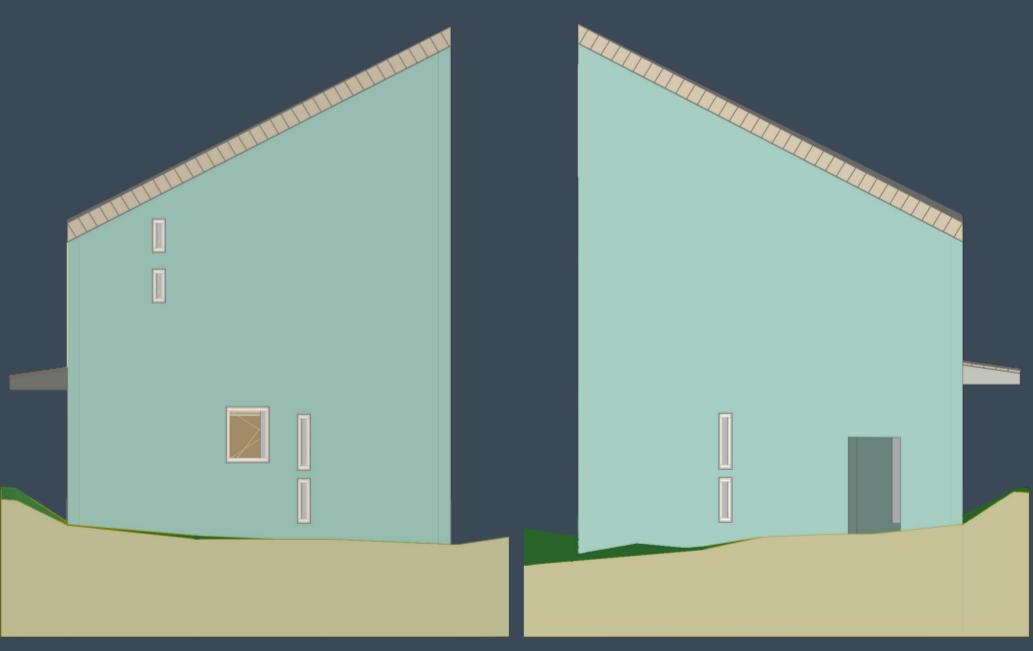

South-west elevation

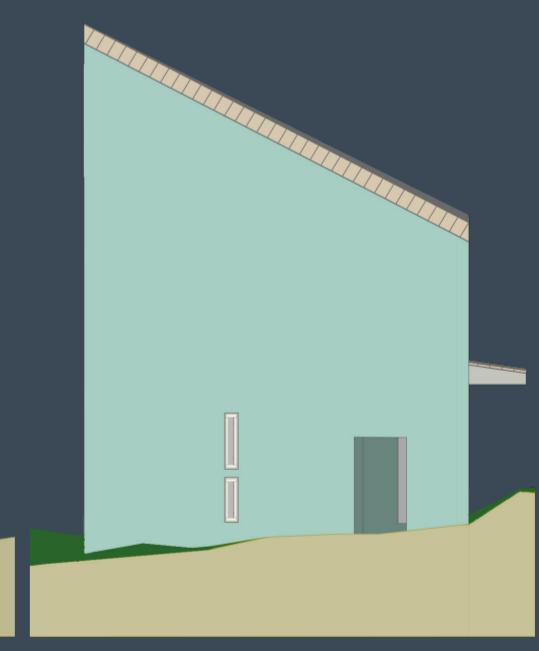


North-east elevation



POLITECNICO DI MILANO | SCUOLA DEL DESIGN
CORSO DI LAUREA IN DESIGN DEGLI INTERNI
LABORATORIO DI STRUMENTI E METODI DEL
PROGETTO
| A.A. 2017-18 | SEZ. I2

DERIU MARIA GIOVANNA 892967
TOLOTTI NOEMI 893094

TAVOLA 1

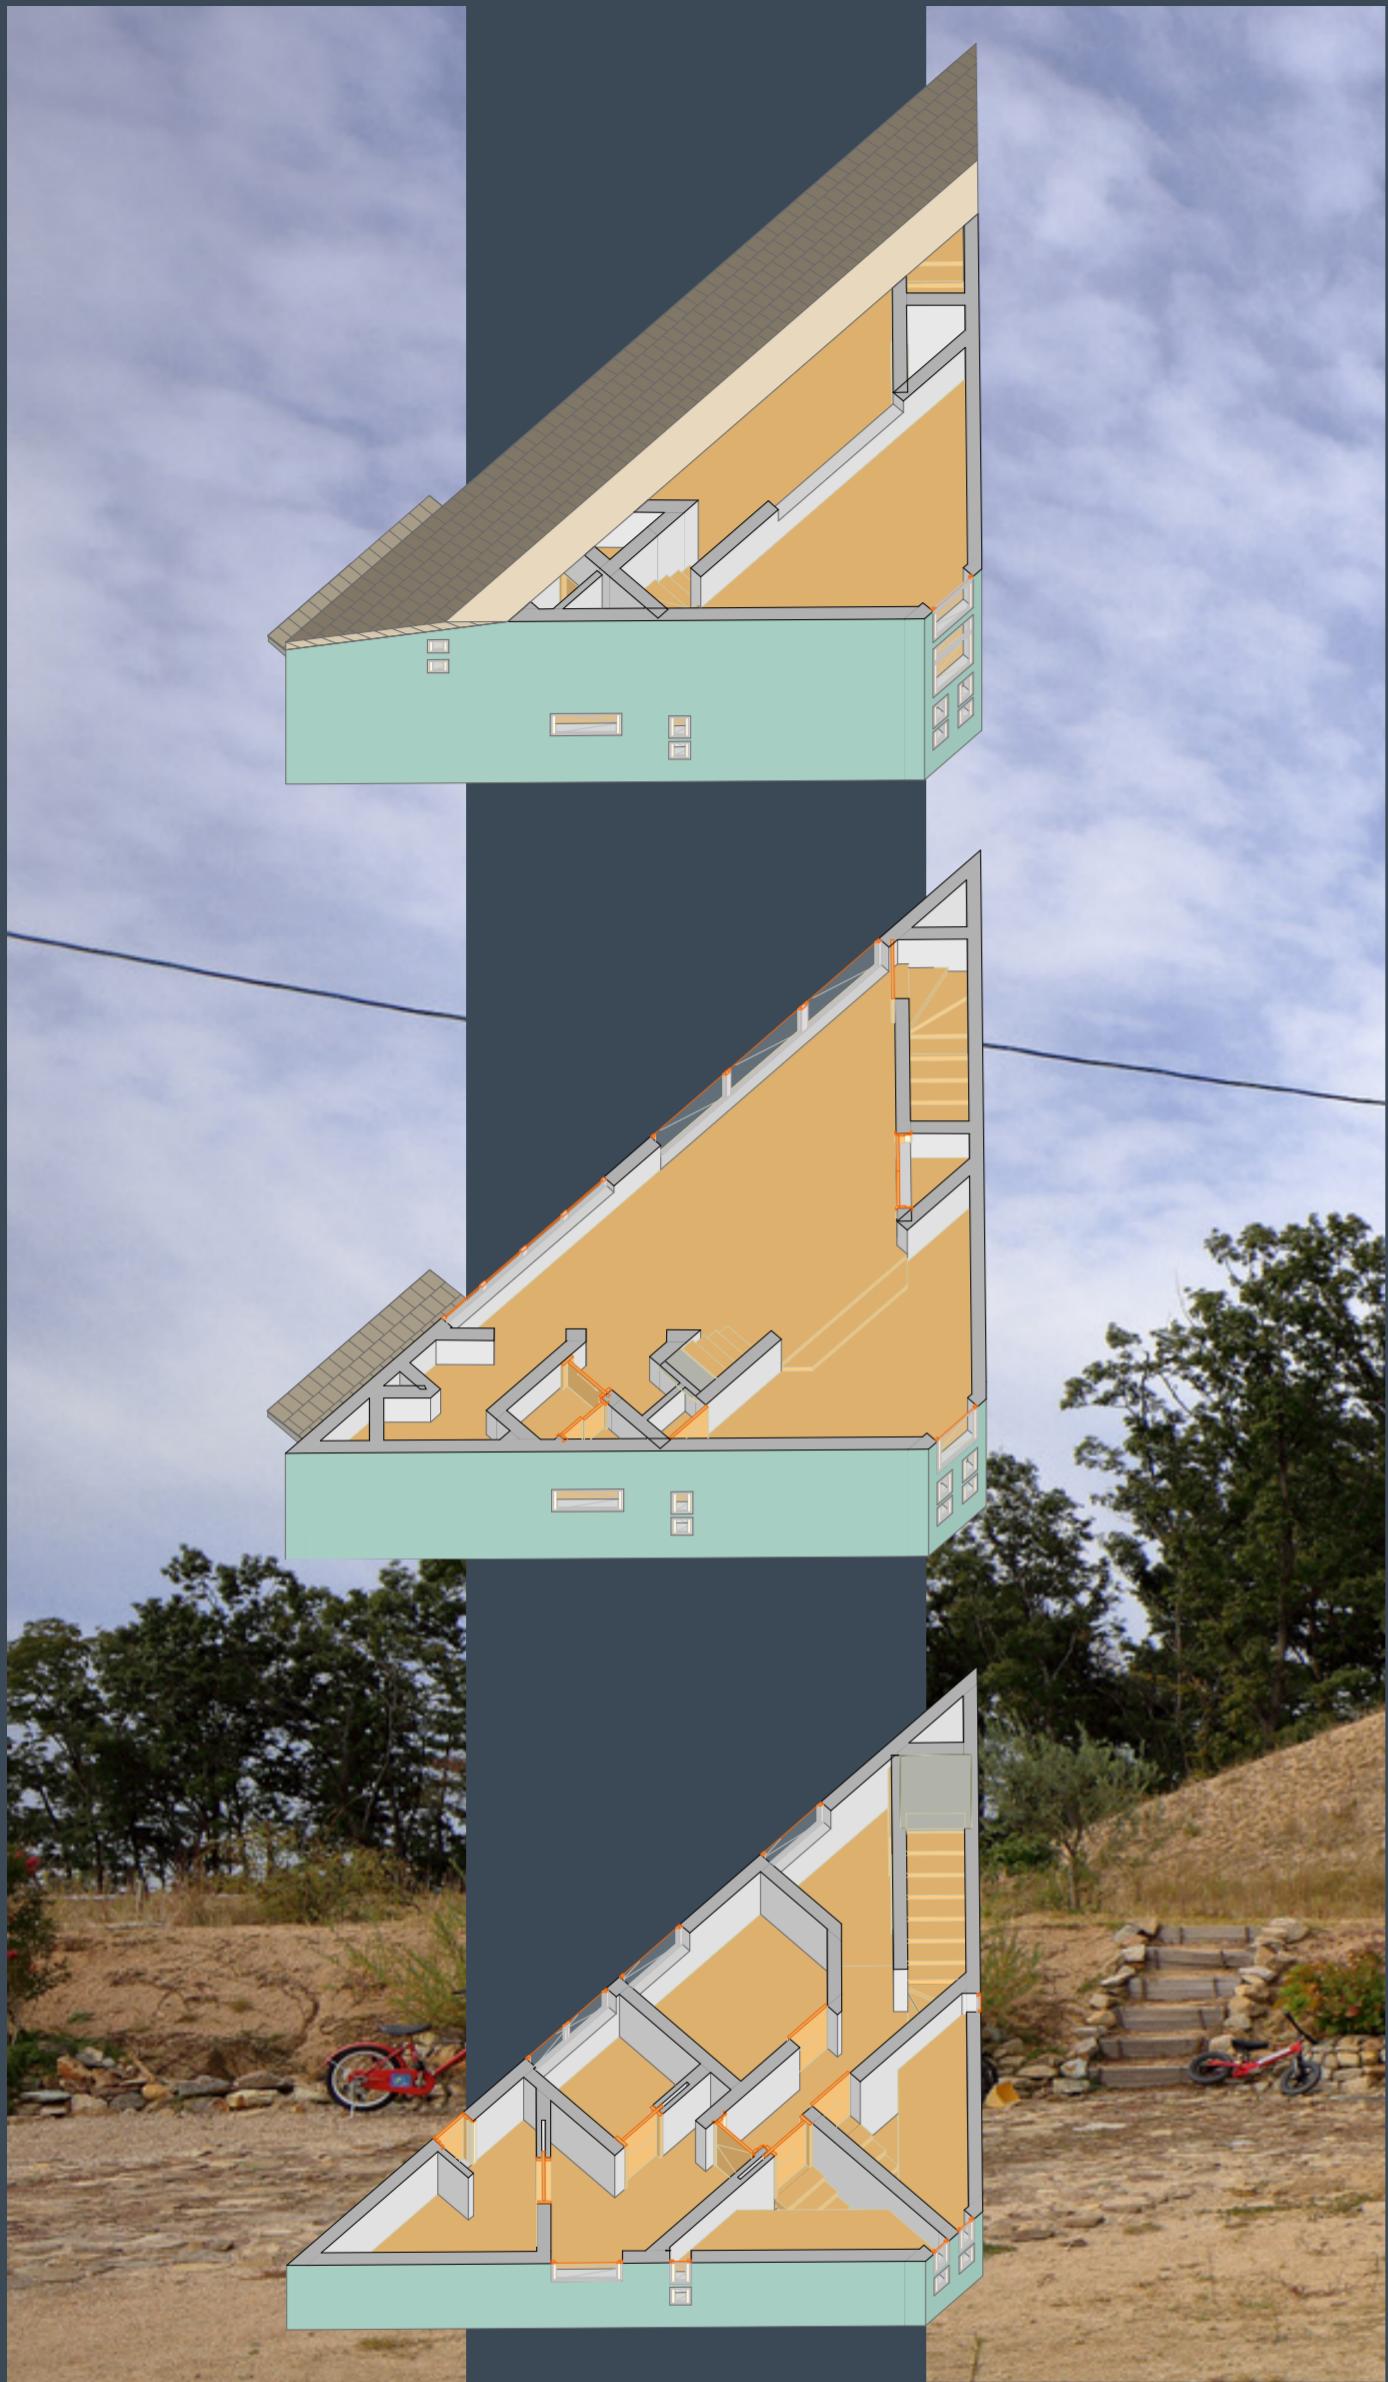

The site for this project is located at the corner of building lots provided by cutting through a hilly topography. The ground level of this site is higher among other lots, and next to the site in the north side of the building is a slope of a designated green area of the building lots. According to the site with irregular shape, the building is configured in a triangular form. From the inside of the building, exterior view is provided to the slope covered with greenery on the north side of the lot.


A bedroom, a room for children, a lavatory, and a bathroom are allocated on the 1st floor, while a living room, a dining room, and a kitchen are gathered on the 2nd floor. Large windows of the dining room and the living room allow clear view to the north side of the lot. The 3rd floor houses a guest room in a traditional Japanese style, which can be also used as a bedroom or a living room.

The kitchen has an open layout with L-shaped configuration, which allows this space to become the center of this house by enjoying cooking while seeing the scenery, or having conversation with family members while cooking, or inviting friends and cooking together at the kitchen.







Section A-A
Scale 1:100

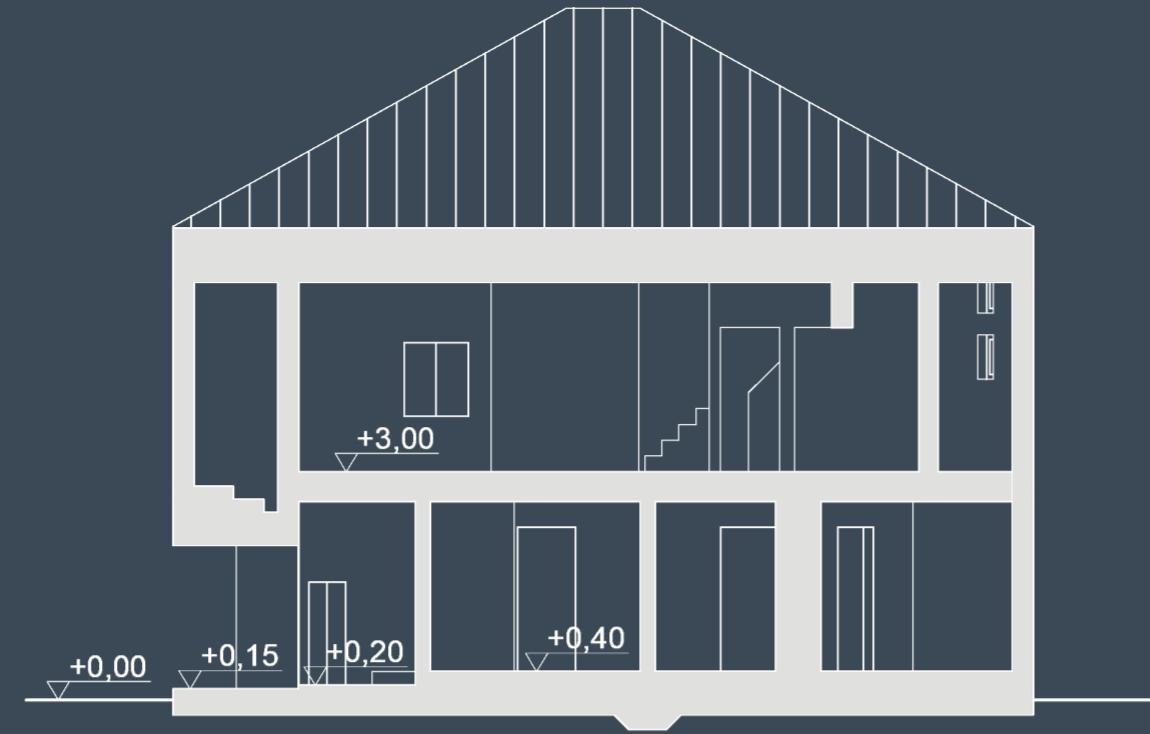

Section B-B
Scale 1:100

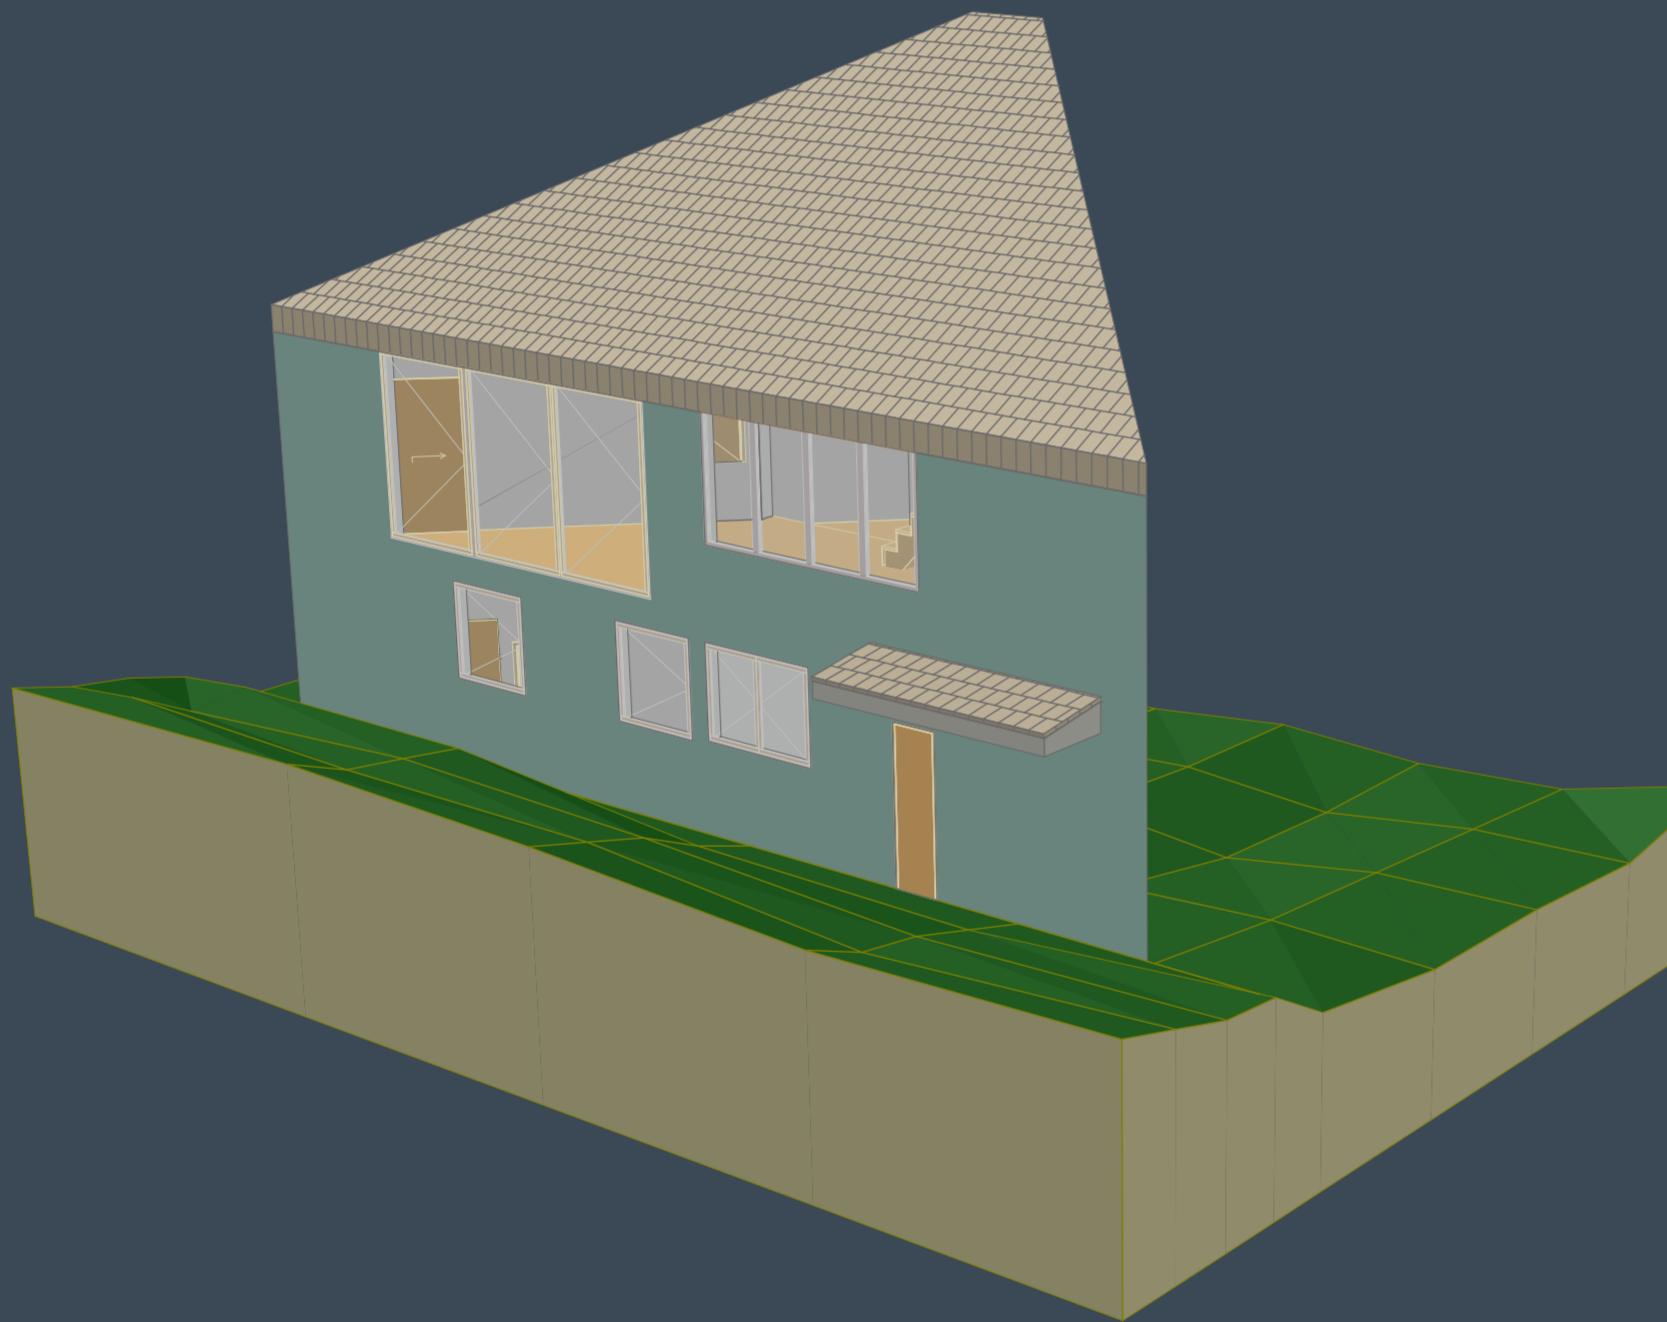

Internal view of the kitchen and the living room

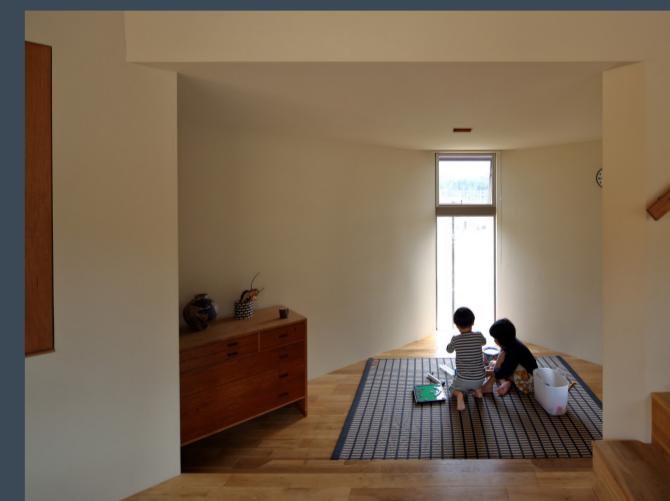

POLITECNICO DI MILANO | SCUOLA DEL DESIGN
CORSO DI LAUREA IN DESIGN DEGLI INTERNI
LABORATORIO DI STRUMENTI E METODI DEL
PROGETTO
| A.A. 2017-18 | SEZ. I2

DERIU MARIA GIOVANNA 892967
TOLOTTI NOEMI 893094

TAVOLA 3