

Casa en l'Armentera

Casanovas, Graus, Pérez

LOCALIZZAZIONE: L'Armentera, Spagna

ARCHITETTI: Casanovas, Graus, Pérez

SUPERFICIE: 168.0 m²

ANNO: 2017

COSTRUTTORE: Burgos Gasull

L'Armentera è un piccolo villaggio vicino alle paludi di Empordà, in Costa Brava. Nel 2005 venne attuato un piano urbano nella zona sud del villaggio e molti dei suoi terreni agricoli diventarono edificabili. La casa occupa uno di questi lotti.

Il progetto si proponeva di rispondere a due principali domande:

- Come evitare l'estrema vicinanza di case esistenti e future;
- Come riparare dalla Tramontana, il potente vento dal nord dei Pirenei, e come nel frattempo sfruttare al meglio il sole e la Marinada, il vento di mare che rinfresca la casa d'estate.

La risposta a queste domande è sintetizzata nella forma a "L" dell'edificio, che organizza i suoi spazi principali attorno al giardino e alla piscina. Questa forma consente alla casa di essere protetta dal vento freddo e dalla strada e allo stesso tempo permette di non rinunciare ad un'ottima esposizione solare.


Al primo piano, le facciate apparentemente cieche evitano la vicinanza alle finestre delle case a fianco attraverso la creazione di un patio che riempie di luce l'interno.

I materiali sono lasciati "al naturale", anche le tubature di rame sono trattate come un materiale esposto.


L'uso di pannelli di protezione solare realizzati con rattan intrecciato davanti alle finestre fornisce un piacevole controllo della luce e una fresca ventilazione naturale che evita la necessità di un impianto di climatizzazione in estate e il riscaldamento è prodotto da un sistema aerotermico.

Il giardino è costruito intorno ad una piccola piscina sollevata che diventa una lunga panchina, la privacy è garantita con la crescita della vegetazione oltre la recinzione perimetrale.




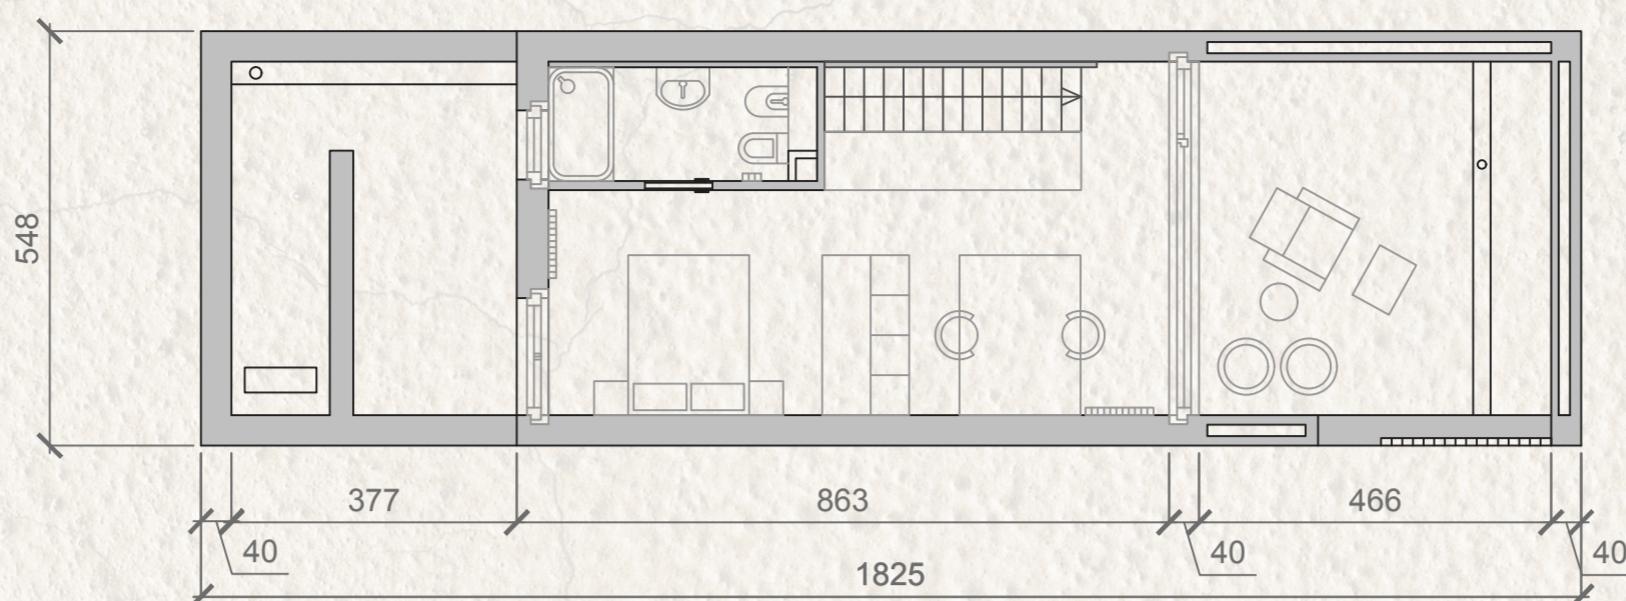


Pianta primo piano, scala 1:100

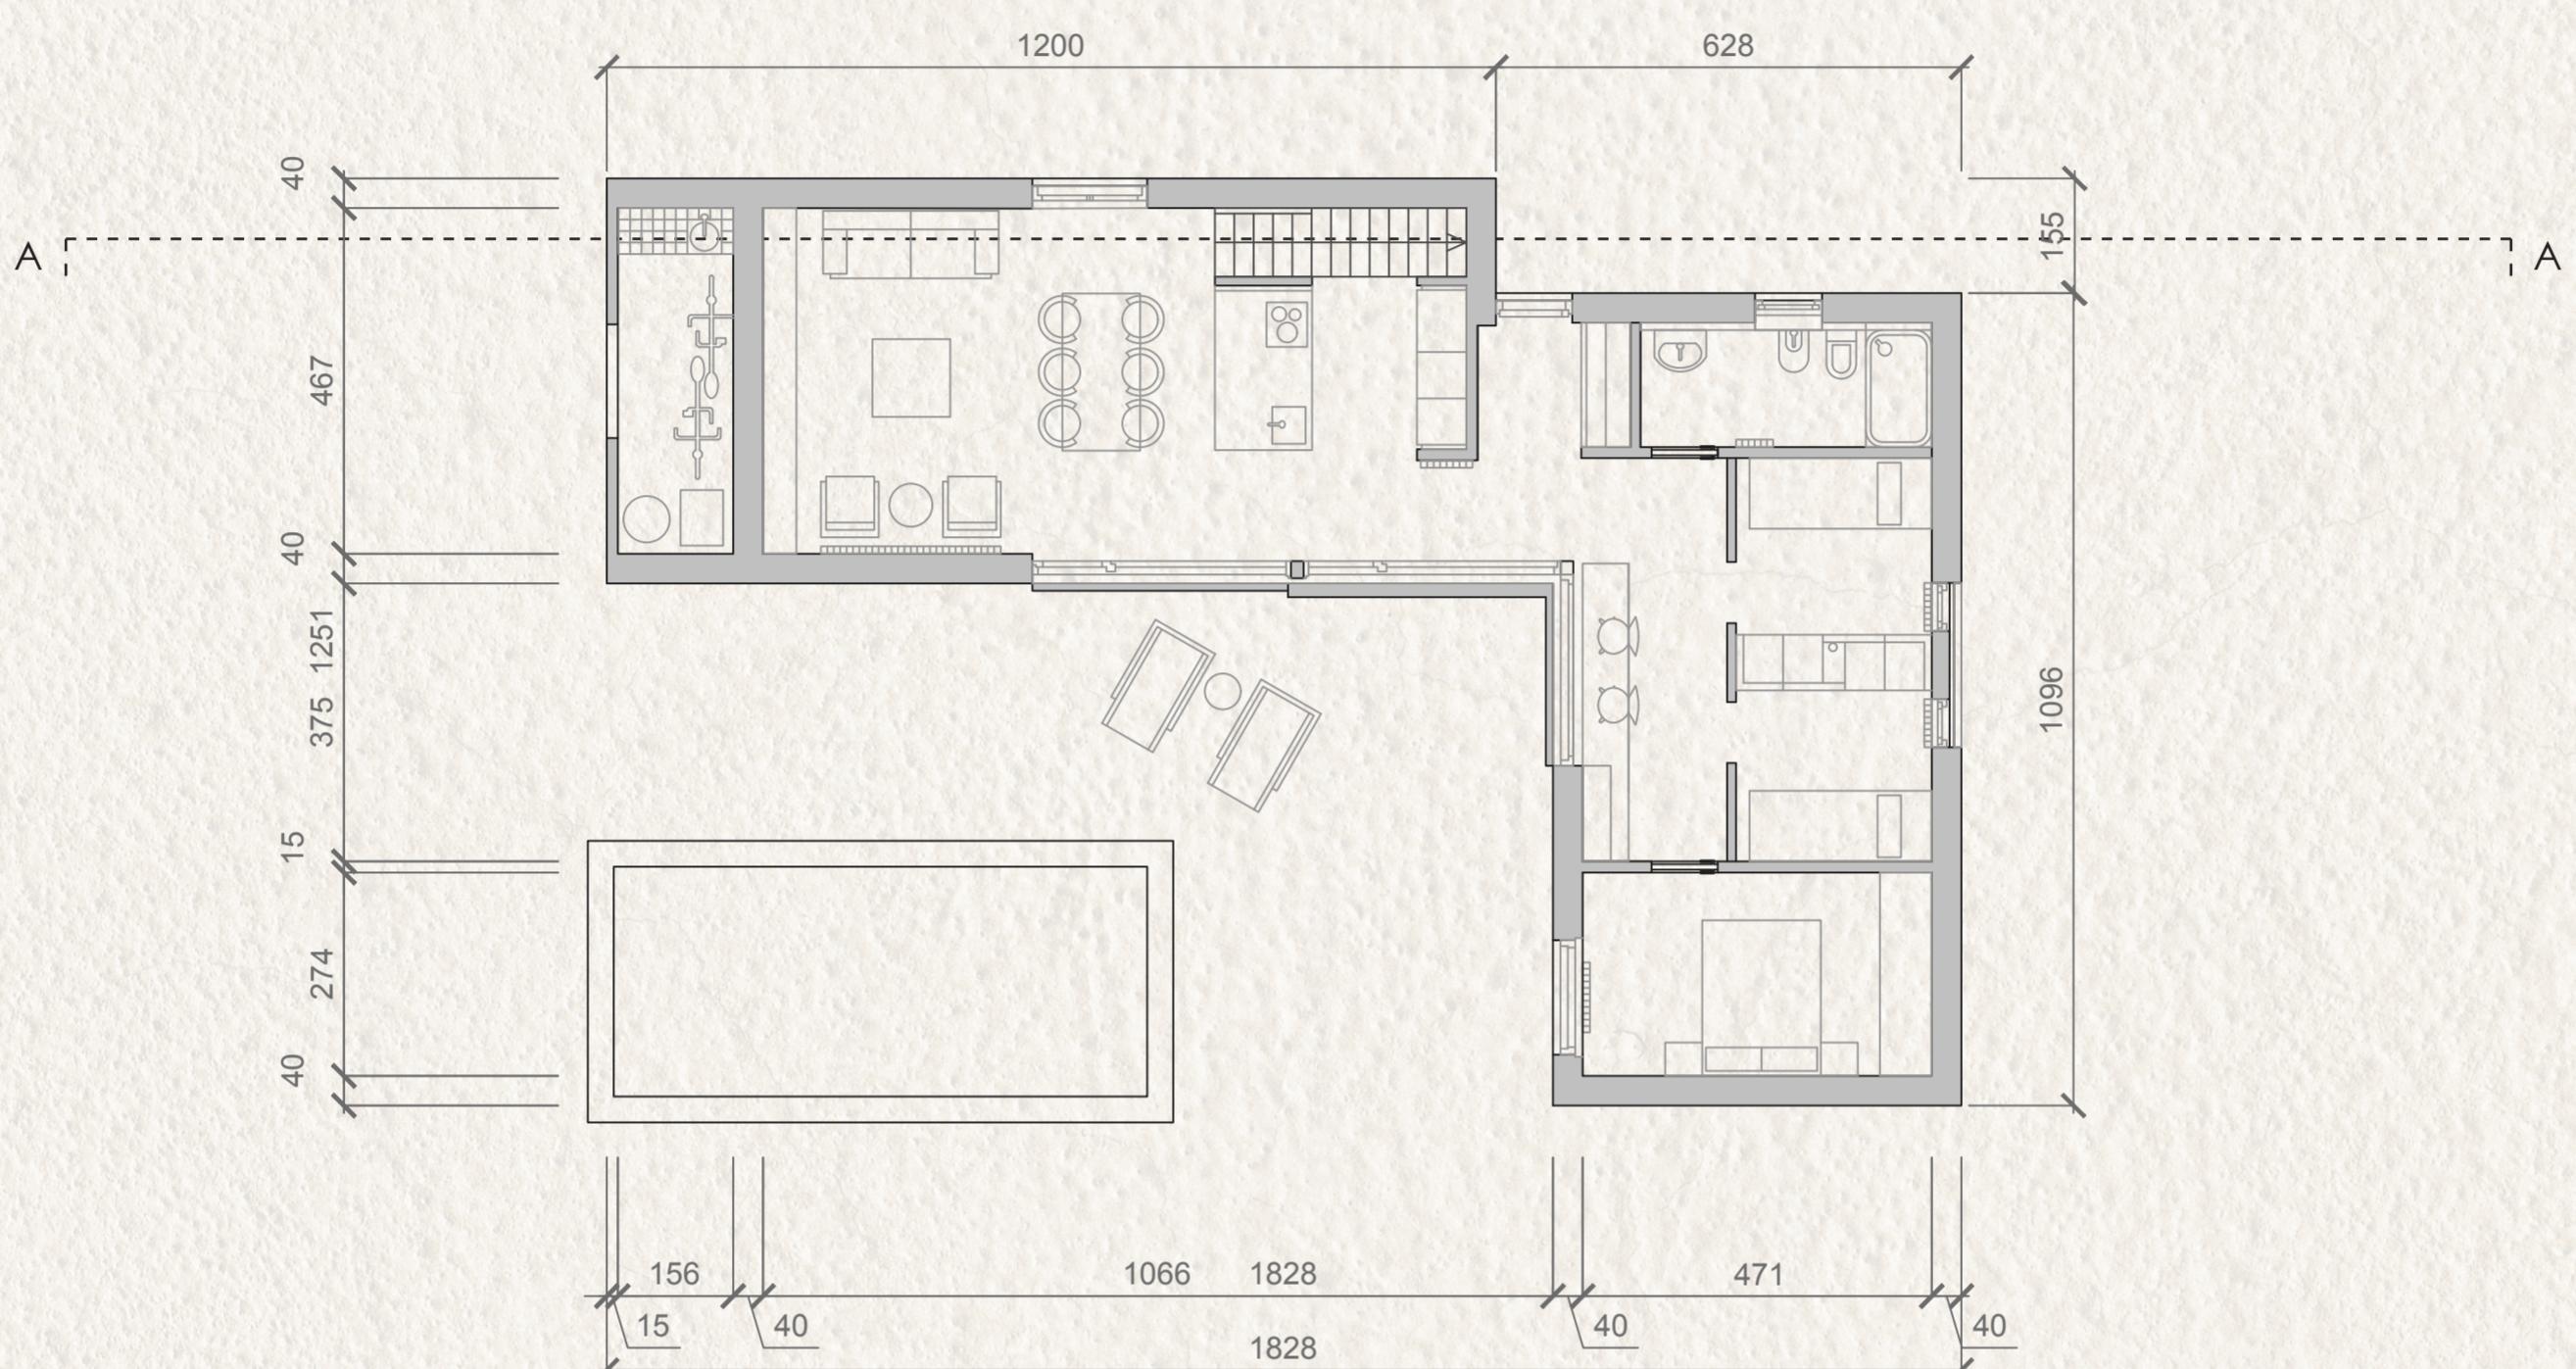

Pianta piano terra, scala 1:100

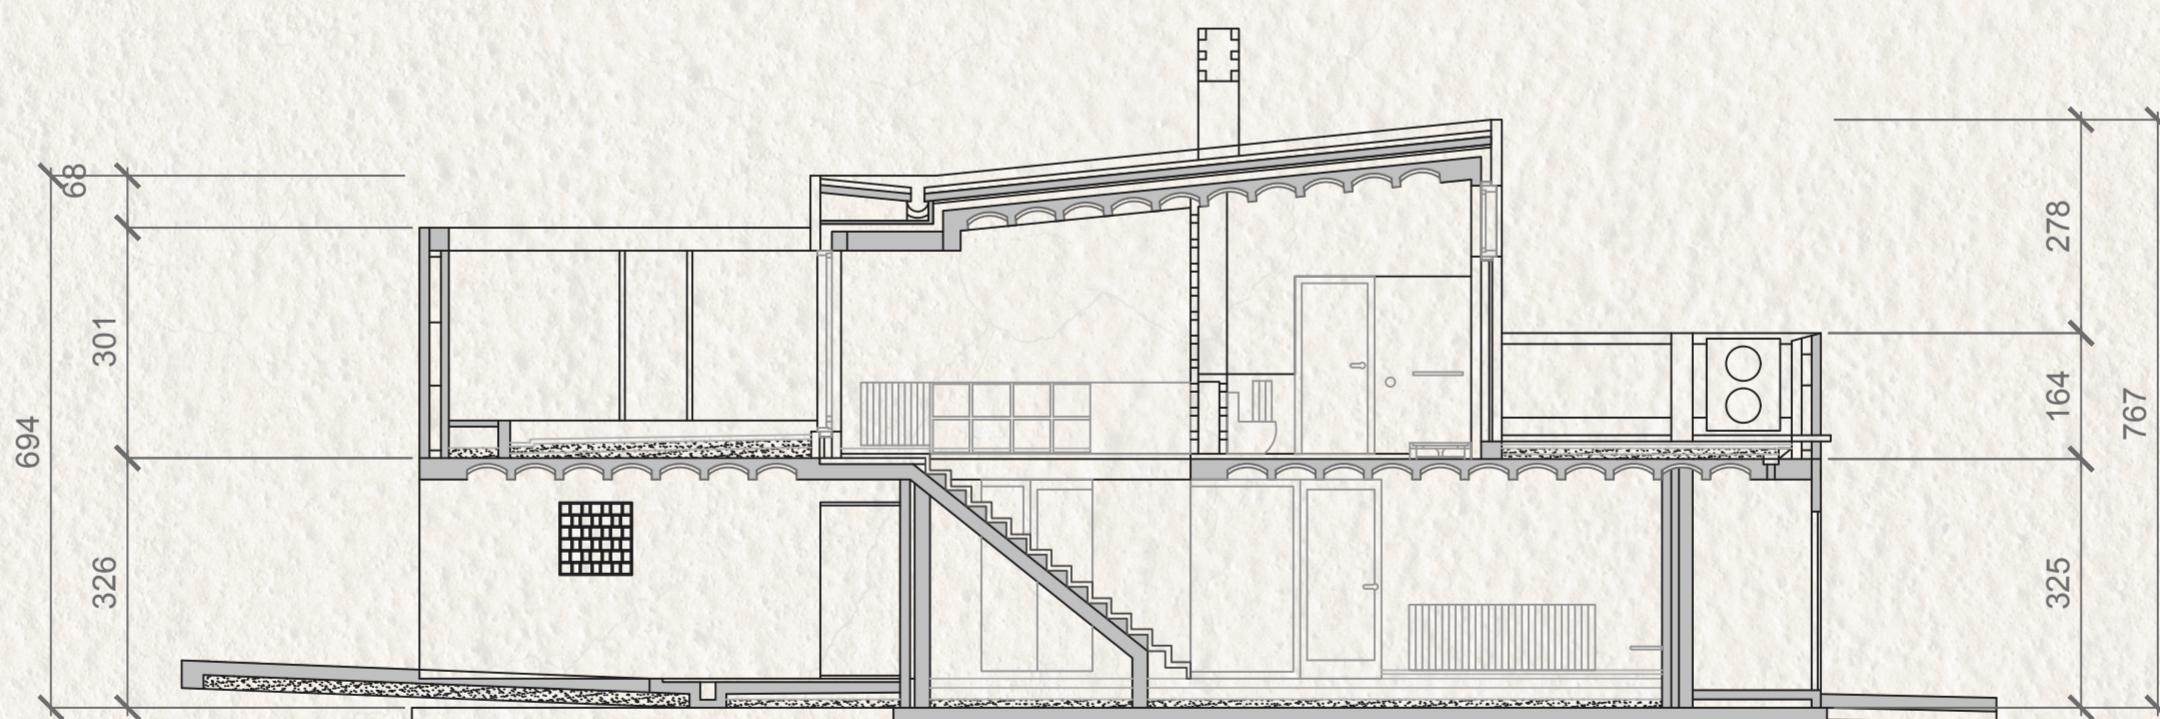

Sezione AA, scala 1:100

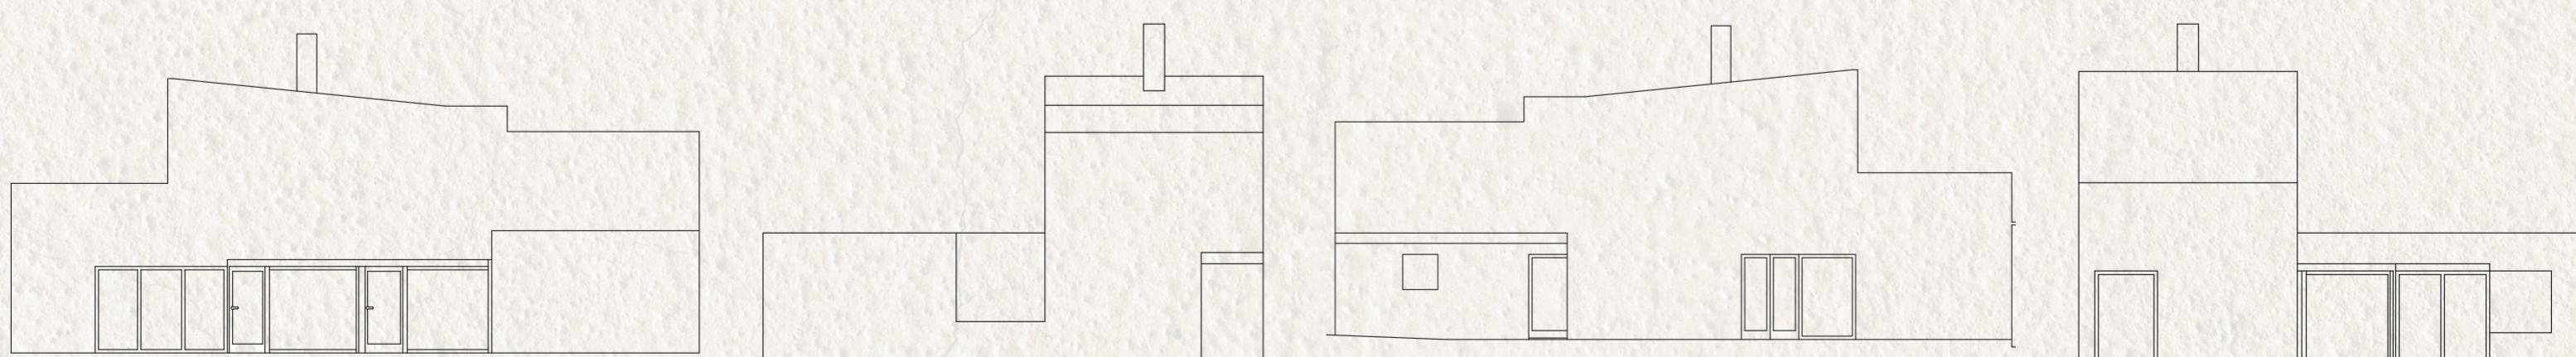

Prospetti Nord, Ovest, Sud, Est



Render assonometrico

Nei tondi, da sinistra a destra:
Cucina piano terra (foto)
Camera da letto matrimoniale
Camera da letto bambini